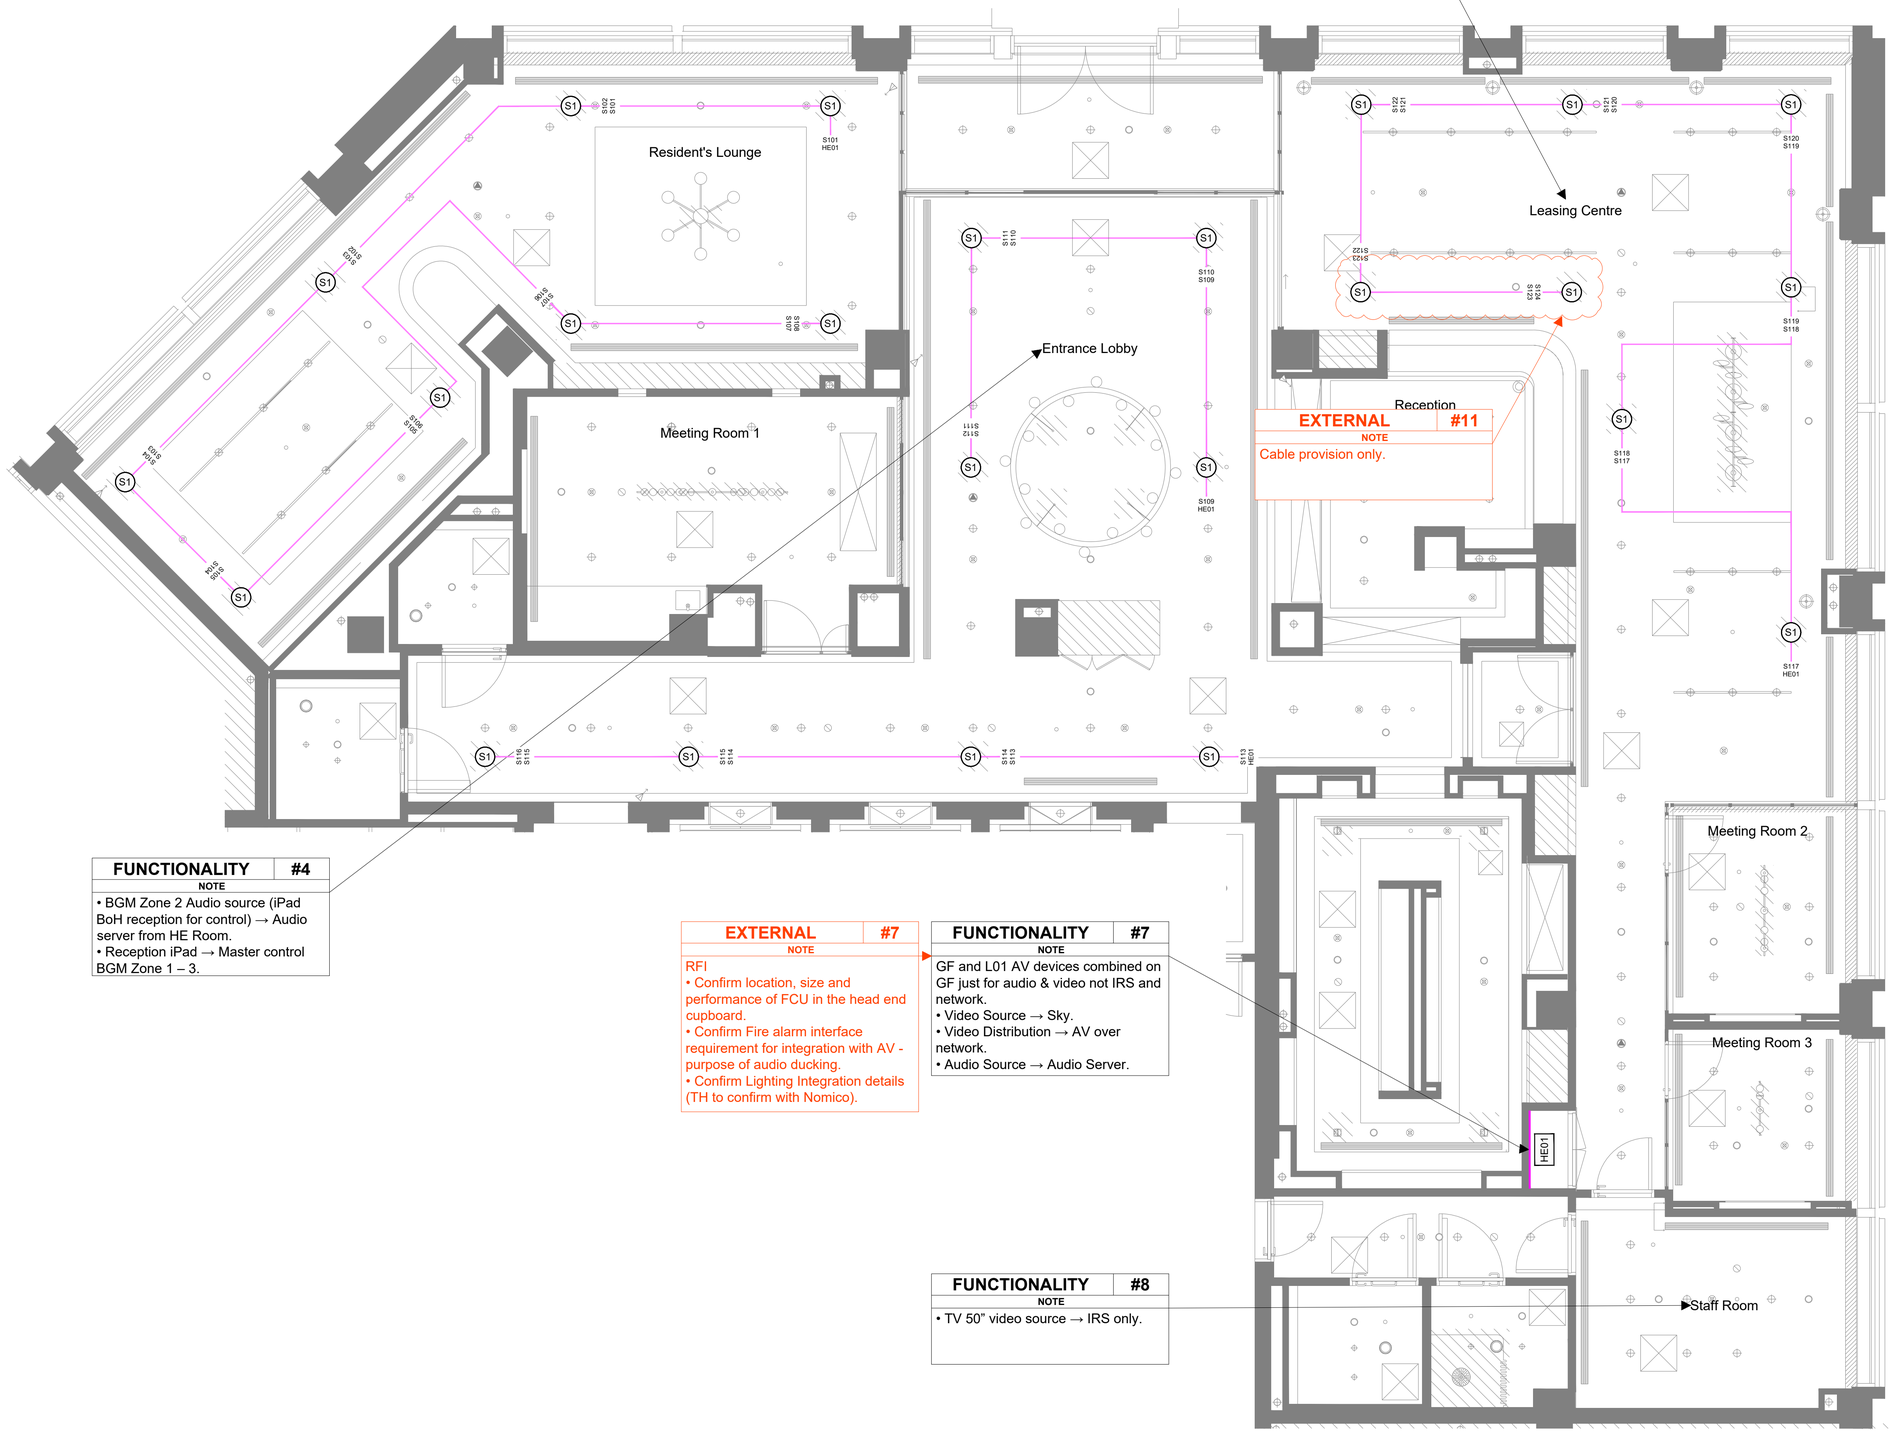

EXTERNAL	#2
NOTE	
RFI None	

FUNCTIONALITY	#2
NOTE	
• BGM Zone 3 Audio source → Audio server from HE Room. • Touch Panel 7" (TP06) → Room control for BGM Zone 3.	

FUNCTIONALITY	#4
NOTE	
• BGM Zone 2 Audio source (iPad BoH reception for control) → Audio server from HE Room. • Reception iPad → Master control BGM Zone 1 – 3.	

EXTERNAL	#7
NOTE	
RFI • Confirm location, size and performance of FCU in the head end cupboard. • Confirm Fire alarm interface requirement for integration with AV - purpose of audio ducking. • Confirm Lighting Integration details (TH to confirm with Nomico).	

FUNCTIONALITY	#7
NOTE	
GF and L01 AV devices combined on GF just for audio & video not IRS and network. • Video Source → Sky. • Video Distribution → AV over network. • Audio Source → Audio Server.	

FUNCTIONALITY	#8
NOTE	
• TV 50" video source → IRS only.	

EXTERNAL	#11
NOTE	
Cable provision only.	

NOTES

Reference Drawings

17010_AAM_BD_00_DR_A_06401.P7.8 (RCP)

LEGEND

Item Example

M1 — "M1" Wall Mounted Media Plate 01
"Cables" 2x CAT6A
M102 HE01 — "M1" Item ID "02" Unique Number "HE01" Head End

Head End Equipment

HExx — Wall Rack
By Others
- IRS Aerial Feed(s)
- LV (230V) Power
- Fire Alarm Interface(s)
- HVAC Cooling
- Landlords Network Connection(s)

Wall Mounted Equipment

M1 — Media Plate 01
By Others
- IRS Aerial Feed(s)
- LV(230V) Power

M6 — Media Plate 06

RB — Room Booking Panel

TP — Touch Panel

FP — Fire Place

Speaker Types

S1 — Speaker Type 1 - Ceiling
S2 — Speaker Type 2 - Wall Mount
S3 — Speaker Type 3 - External
S4 — Speaker Type 4 - External
S5 — Speaker Type 5 - External Wall Mount
S6 — Speaker Type 6 - External Wall Mount
S7 — Speaker Type 7 - External Subwoofer
S8 — Speaker Type 8 - Soundbar

Floorboxes

FB — Floorbox

Cable Types

Speaker Cable TBC
CAT6a Cable F/FTP Nexans [N100.692G-OC]
WF100 Digital Coaxial Cable Webro [392100HCAI]
Cresnet Control Cable Crestron [Cresnet-P-TL-SP1000]

For Construction

© Copyright. All rights to this drawing and its design are the property of SmartComm Ltd. Any use or duplication of this drawing is strictly prohibited without prior written permission of SmartComm Ltd.

Drawn By	SD	22/07/22
Checked By	SK	22/07/22
Issued By	BW	22/07/22
SCALE	NTS	
PAGE SIZE	A1	

smartcomm
integrating technology with vision

Smartcomm Ltd
Halifax Road
Cressex Business Park
High Wycombe
Buckinghamshire
HP12 3SN

Tel: +44 (0)1494 471 912
E-mail: info@smartcomm.co.uk
Web: www.smartcomm.co.uk

Rev	Description	Date	Name
C03	For Construction	22/07/22	SD
C02	For Construction	29/04/22	SD
C01	For Construction	20/10/21	SD
A02	For Approval	29/07/21	CL
A01	For Approval	29/06/21	CL

Royal Mail Parkside
Block D - Level 00
AV Layout - High Level

Project	Section	Type	Number	Revision	Version
NEPS	BD-00	GA	11	C03	V05