

FUNCTIONALITY	#3
NOTE	
• N°4 TV 43" video source (M102 - M105) → IRS and Video Distribution. • BGM Zone 1 Audio source → Audio source from HE Room GF. • Touch Panel 5" (TP02 BoH) → Master control BGM Zone 1 – 3 and local TVs.	

EXTERNAL	#1
NOTE	
RFI • Client request no SKY required but Freeview. Not Freeview distribution but each TV its own decoder. • Confirm screen in Omnia Room and requirement for technogym connection.	

FUNCTIONALITY	#1
NOTE	
• N°1 TV 65" video source (M106) → IRS only and Local source (HDMI). • BGM Zone 1 Audio source → Audio source from HE Room GF.	


EXTERNAL	#2
NOTE	
Location / Setting Out TBA. No Decoder but cable only. Hardware out of scope due to VE.	

FUNCTIONALITY	#4
NOTE	
GF and L01 AV devices for audio & video combined into GF. L01 AV cupboard for IRS and network. • Video Source → Sky. • Video Distribution → AV over network cable. • Audio Source → GF Audio source.	

EXTERNAL	#4
NOTE	
RFI • Confirm location, size and performance of FCU in the head end cupboard. • Confirm Fire alarm interface requirement for integration with AV - purpose of audio ducking. • Confirm Lighting Integration details (TH to confirm with Nomico).	

COORDINATION	#6
NOTE	
Refer to RFI R001942	

FUNCTIONALITY	#5
NOTE	
• TV 43" video source (M101) → IRS source only. • Soundbar (S601) → TV sound only. • Touch Panel 5" (TP01) → Room control for TV.	

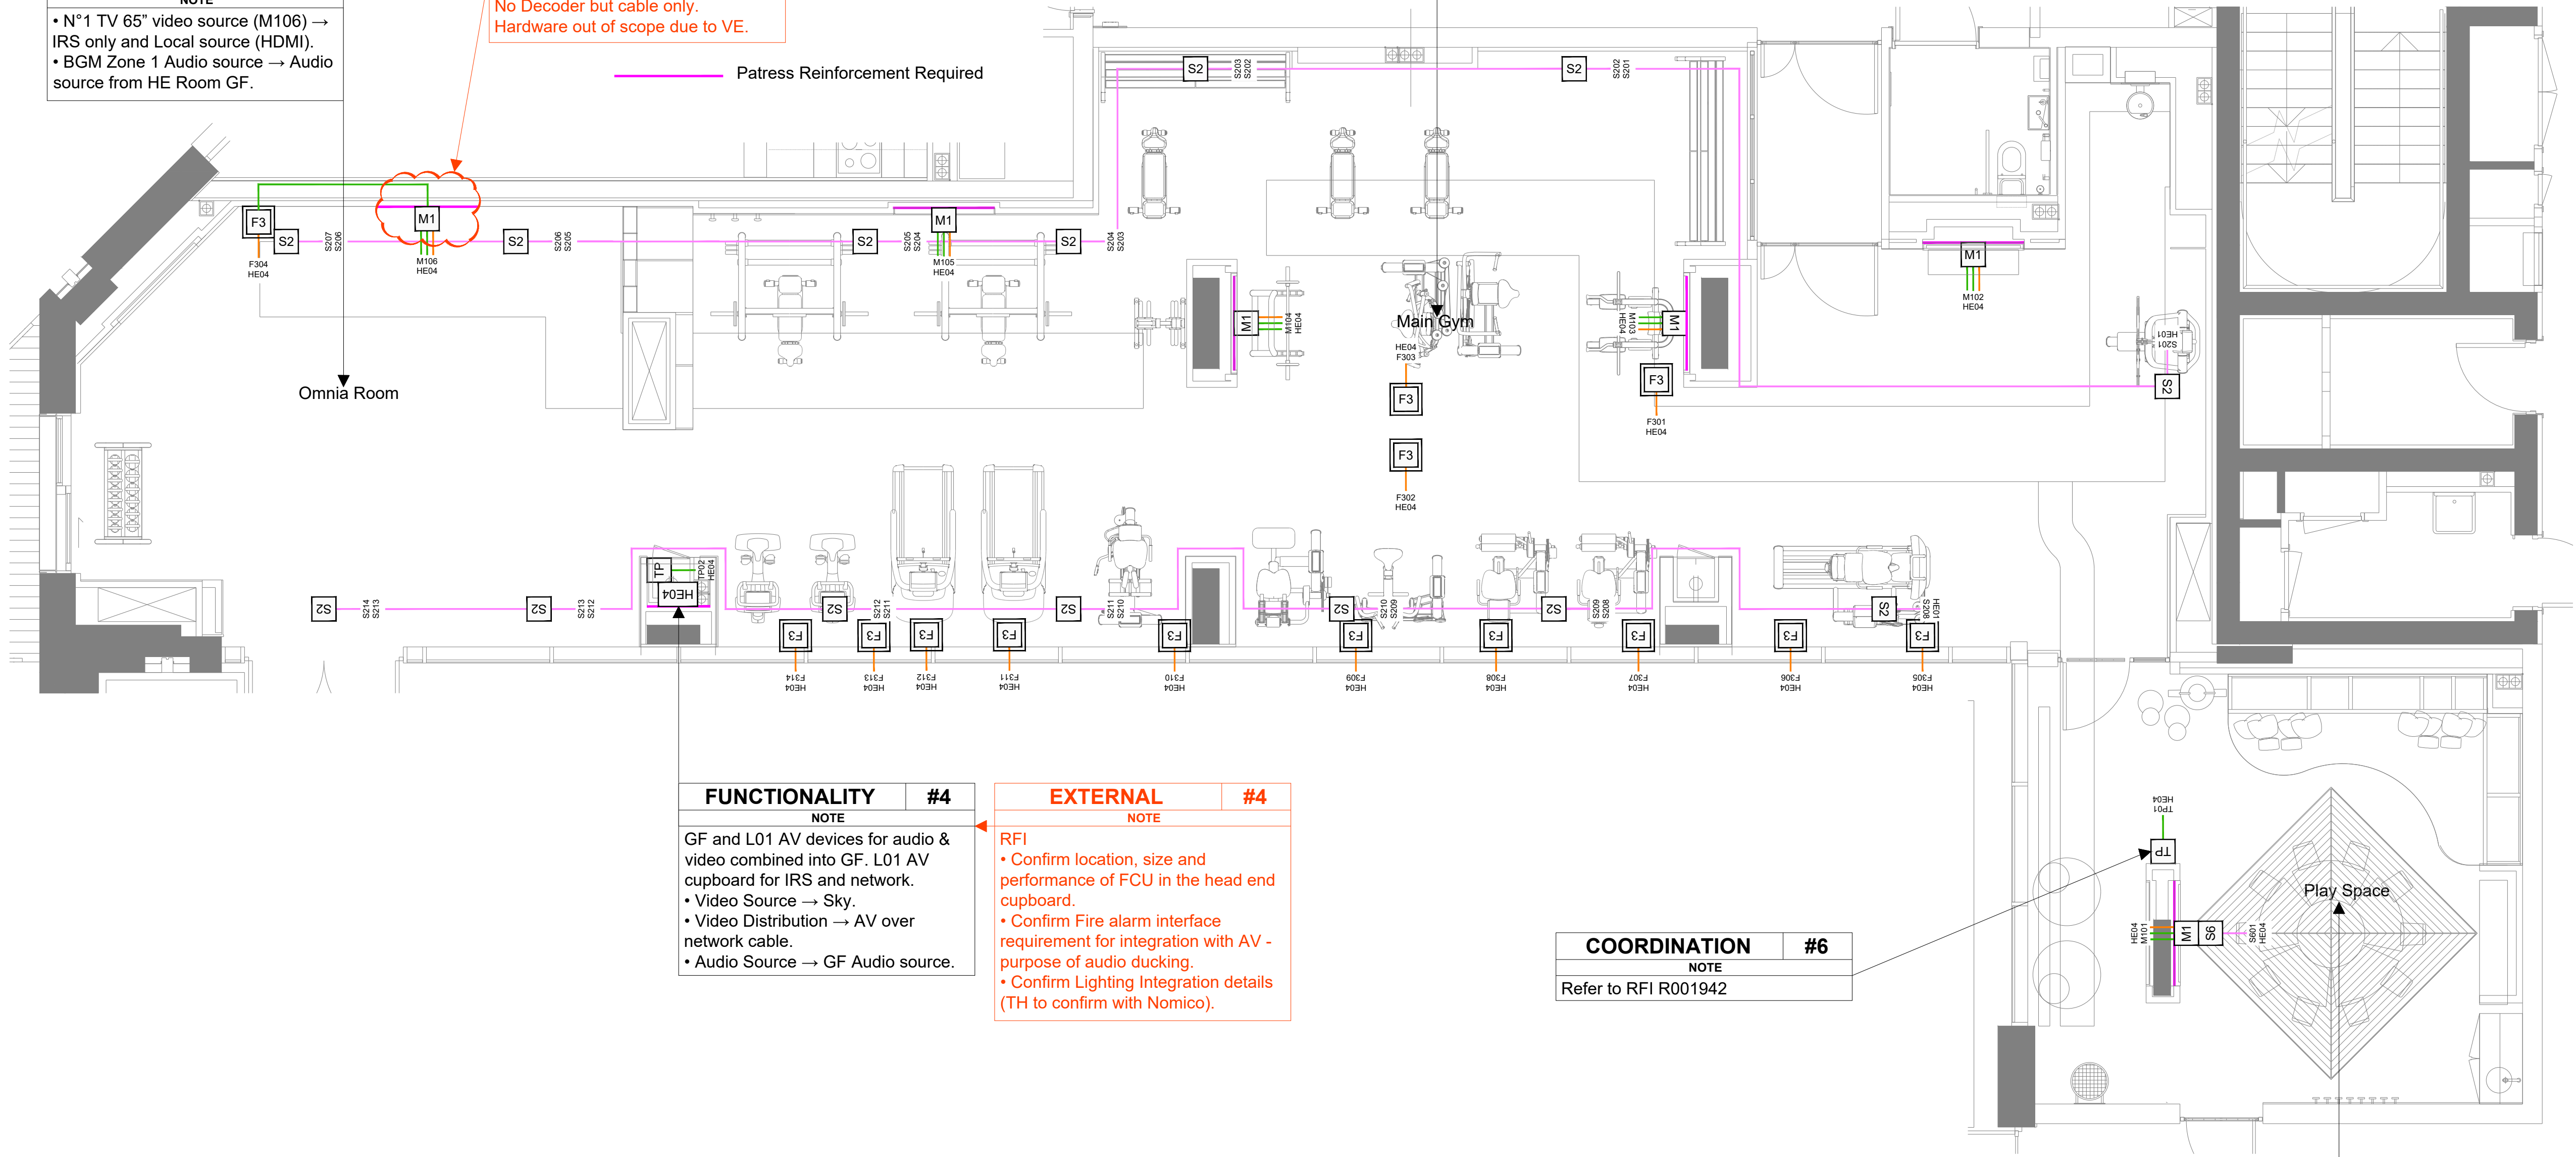

NOTES

Reference Drawings

17010_AAM_BD_01_DR_A_06101.C13.21 (GA)

LEGEND

Item Example

M102
HE01
"M1" Wall Mounted Media Plate 01
"Cables" 2x CAT6A
"M1" Item ID "02" Unique Number
"HE01" Head End

Head End Equipment

HExx Wall Rack
By Others
• IRS Aerial Feed(s)
• LV (230V) Power
• Fire Alarm Interface(s)
• HVAC Cooling
• Landlords Network Connection(s)

Wall Mounted Equipment

M1 Media Plate 01
By Others
• IRS Aerial Feed(s)
• LV (230V) Power
M6 Media Plate 06
RB Room Booking Panel
TP Touch Panel
FP Fire Place

Speaker Types

S1 Speaker Type 1 - Ceiling
S2 Speaker Type 2 - Wall Mount
S3 Speaker Type 3 - External
S4 Speaker Type 4 - External
S5 Speaker Type 5 - External Wall Mount
S6 Speaker Type 6 - External Wall Mount
S7 Speaker Type 7 - External Subwoofer
S8 Speaker Type 8 - Soundbar

Floorboxes

FB Floorbox

Cable Types

Speaker Cable
TBC
CAT6a Cable F/FTP
Nexans [N100.652G-OC]
WF100 Digital Coaxial Cable
Webro [392100HCA]
Crenet Control Cable
Crenet [Crenet-P-TL-SP1000]

For Construction

© Copyright. All rights to this drawing and its design are the property of SmartComm Ltd. Any use or duplication of this drawing is strictly prohibited without prior written permission of SmartComm Ltd.

Drawn By	SD	22/07/22
Checked By	SK	22/07/22
Issued By	BW	22/07/22

SCALE NTS

PAGE SIZE A1



Smartcomm Ltd
Holford Road
Cressex Business Park
High Wycombe
Buckinghamshire
HP12 3SN
Tel: +44 (0)1494 471 912
E-mail: info@smartcomm.co.uk
Web: www.smartcomm.co.uk

Rev	Description	Date	Name
C03	For Construction	22/07/22	SD
C02	For Construction	06/05/22	SD
C01	For Construction	20/10/21	SD
A03	For Approval	31/08/21	CL
A02	For Approval	29/07/21	CL
A01	For Approval	29/06/21	CL

Royal Mail Parkside
Block D Level 01
AV Layout

Project	Section	Type	Number	Revision	Version
NEPS	BD-01	GA	01	C03	V05