


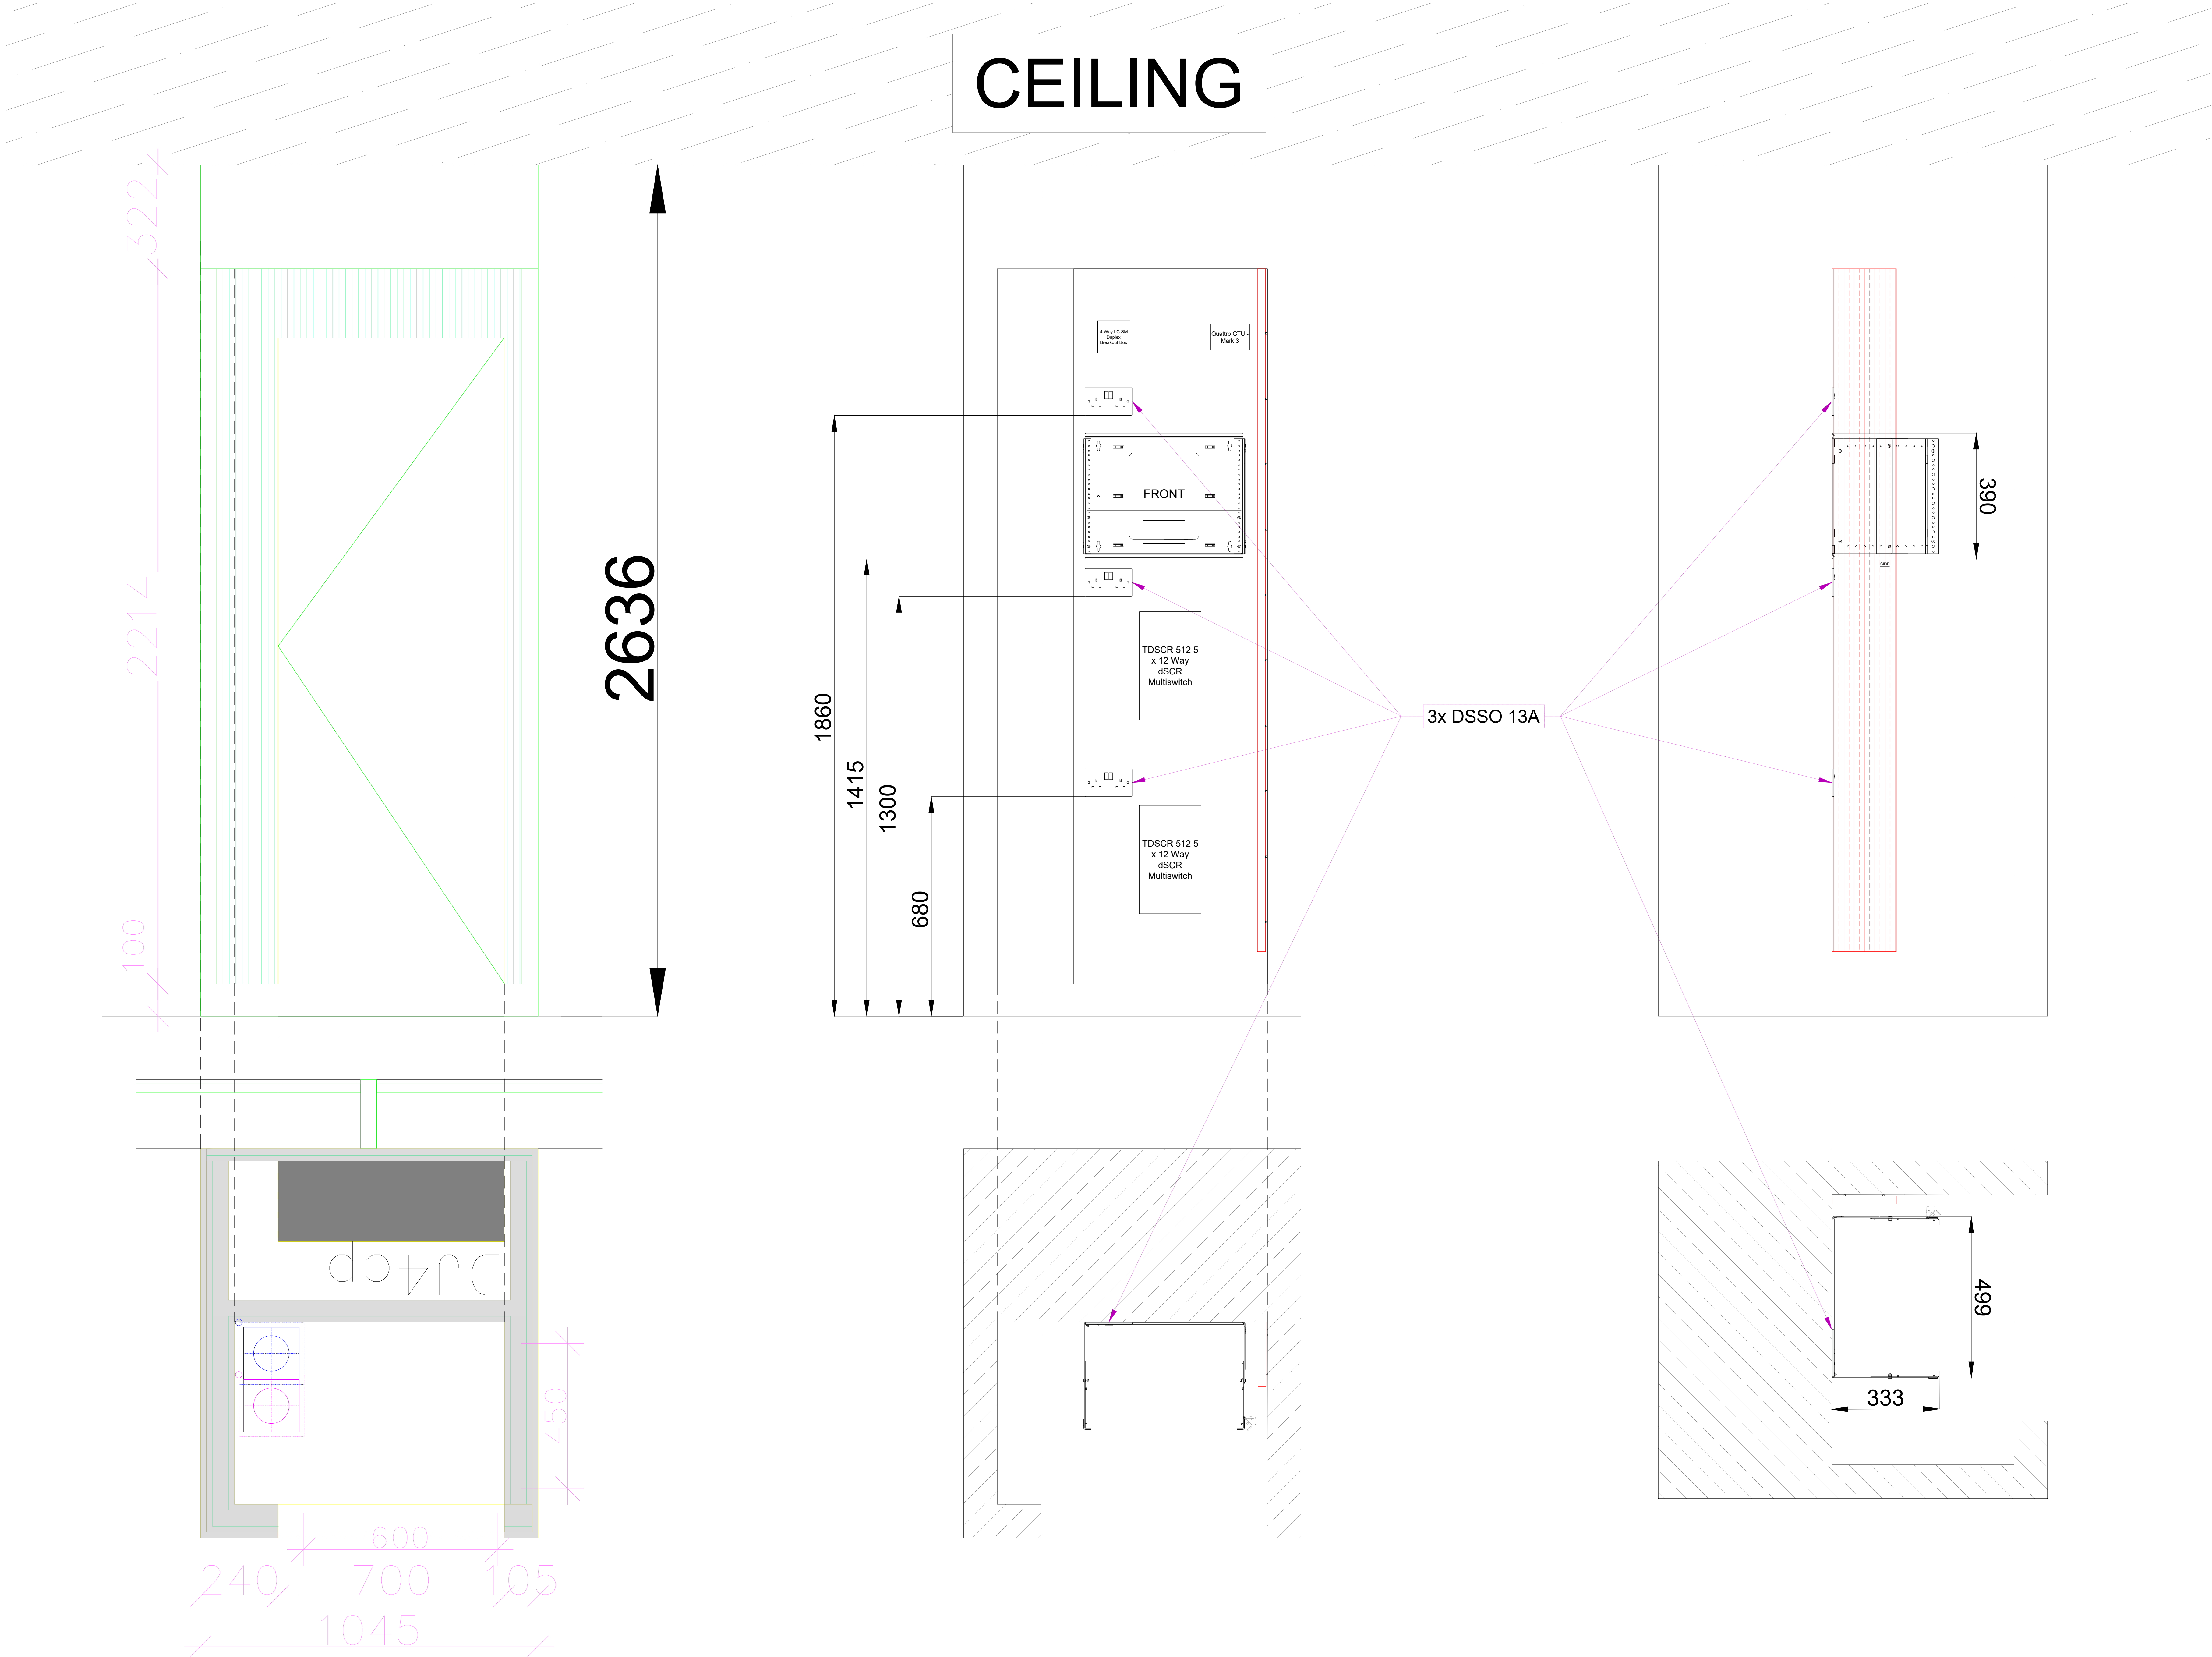

NOTES

The maximum requirement for the L01 Cupboard would be 3 Amps.
The L01 Cupboard is currently around 400 BTU.

LEGEND

FOR APPROVAL

© Copyright. All rights to this drawing and its design are the property of SmartComm Ltd. Any use or duplication of this drawing is strictly prohibited without prior written permission of SmartComm Ltd.

Drawn By	SD	22/07/22
Checked By	SK	22/07/22
Issued By	BW	22/07/22

SCALE NOT TO SCALE

PAGE SIZE A1

smartcomm
integrating technology with vision

Smartcomm Ltd
Halifax Road
Cressex Business Park
High Wycombe
Buckinghamshire
HP12 3SN
Tel: +44 (0)1494 471 912
E-mail: info@smartcomm.co.uk
Web: www.smartcomm.co.uk

A01	For Approval	22/07/22	SD
Rev	Description	Date	Name

Royal Mail Parkside
Block D - Level 01
Rack Elevation - AV cupboard

Project	Section	Type	Number	Revision	Version
NEPS	BD-01	HE	02	A01	V04