


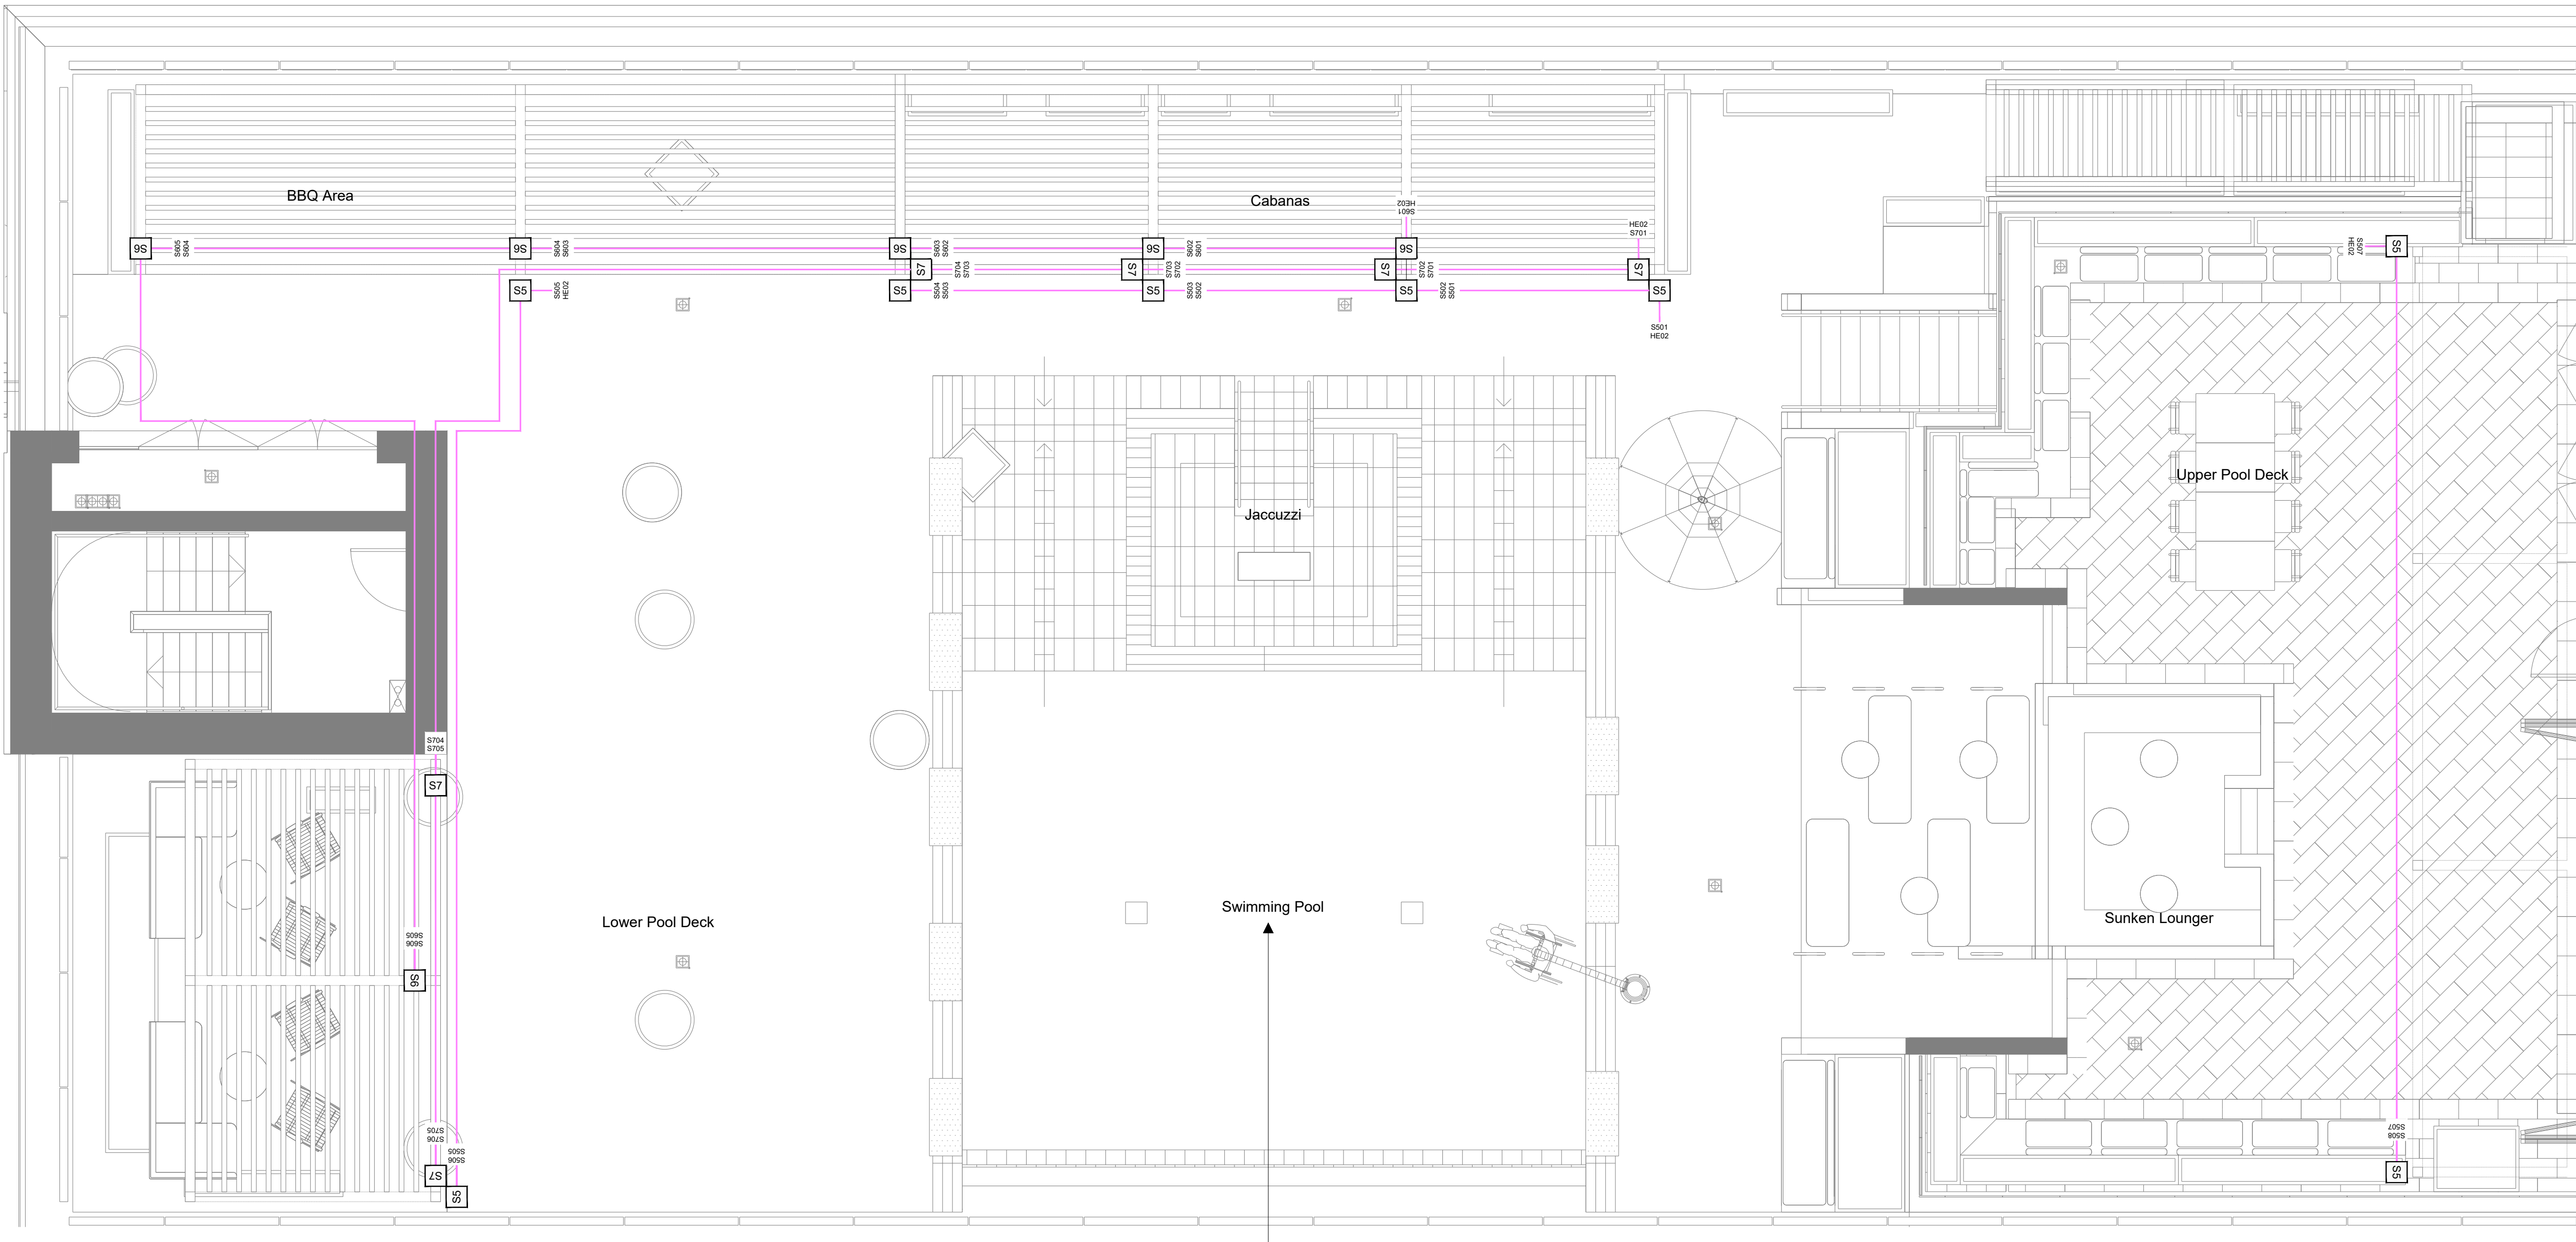

EXTERNAL	#1	FUNCTIONALITY	#1
NOTE		NOTE	
RFI		• Pergola area Audio source BGM Zone 4 → Audio server from HE Room.	
• Confirm speakers proposal.		• Pool area Audio source BGM Zone 5 → Audio server from HE Room.	
• Confirm EXT local audio connection.		• GF Reception iPad to controll Pool area	
• Cable containment TBC by Nomico.			

NOTES

Reference Drawings

17010_AAM_BD_10_DR_A_06110.C12.16 (GA)

LEGEND

Item Example

M1 "M1" Wall Mounted Media Plate 01
M102 "Cables" 2x CAT6A
HE01 "M1" Item ID "02" Unique Number
HE01 "HE01" Head End

Head End Equipment

HExx Wall Rack
By Others
- IRS Aerial Feed(s)
- LV (230V) Power
- Fire Alarm Interface(s)
- HVAC Cooling
- Landlords Network Connection(s)

Wall Mounted Equipment

M1 Media Plate 01
By Others
- IRS Aerial Feed(s)
- LV(230V) Power
M6 Media Plate 06
RB Room Booking Panel
TP Touch Panel
FP Fire Place

Speaker Types

S1 Speaker Type 1 - Ceiling
S2 Speaker Type 2 - Wall Mount
S3 Speaker Type 3 - External
S4 Speaker Type 4 - External
S5 Speaker Type 5 - External Wall Mount
S6 Speaker Type 6 - External Wall Mount
S7 Speaker Type 7 - External Subwoofer
S8 Speaker Type 8 - Soundbar

Floorboxes

FB Floorbox

Cable Types

Speaker Cable
TBC
CAT6a Cable F/FTP
Nexans [N100.692G-OC]
WF100 Digital Coaxial Cable
Webro [392100HCAI]
Cresnet Control Cable
Cresnet [Cresnet-P-TL-SP1000]

For Construction

© Copyright. All rights to this drawing and its design are the property of SmartComm Ltd. Any use or duplication of this drawing is strictly prohibited without prior written permission of SmartComm Ltd.

Drawn By	SD	22/07/22
Checked By	SK	22/07/22
Issued By	BW	22/07/22

SCALE NTS

PAGE SIZE A1

smartcomm
integrating technology with vision

Smartcomm Ltd Haffex Road Cressex Business Park High Wycombe Buckinghamshire HP12 3SN	Tel: +44 (0)1494 471 912 E-mail: info@smartcomm.co.uk Web: www.smartcomm.co.uk
--	--

Rev	Description	Date	Name
C01	For Construction	22/07/22	SD
A04	For Approval	10/05/22	SD
A03	For Approval	26/04/22	SD
A02	For Approval	22/10/21	SD
A01	For Approval	19/08/21	SD

Royal Mail Parkside
Block D Level 10 - Swimming Pool
AV Layout

Project	Section	Type	Number	Revision	Version
NEPS	BD-10	GA	31	C01	V05