


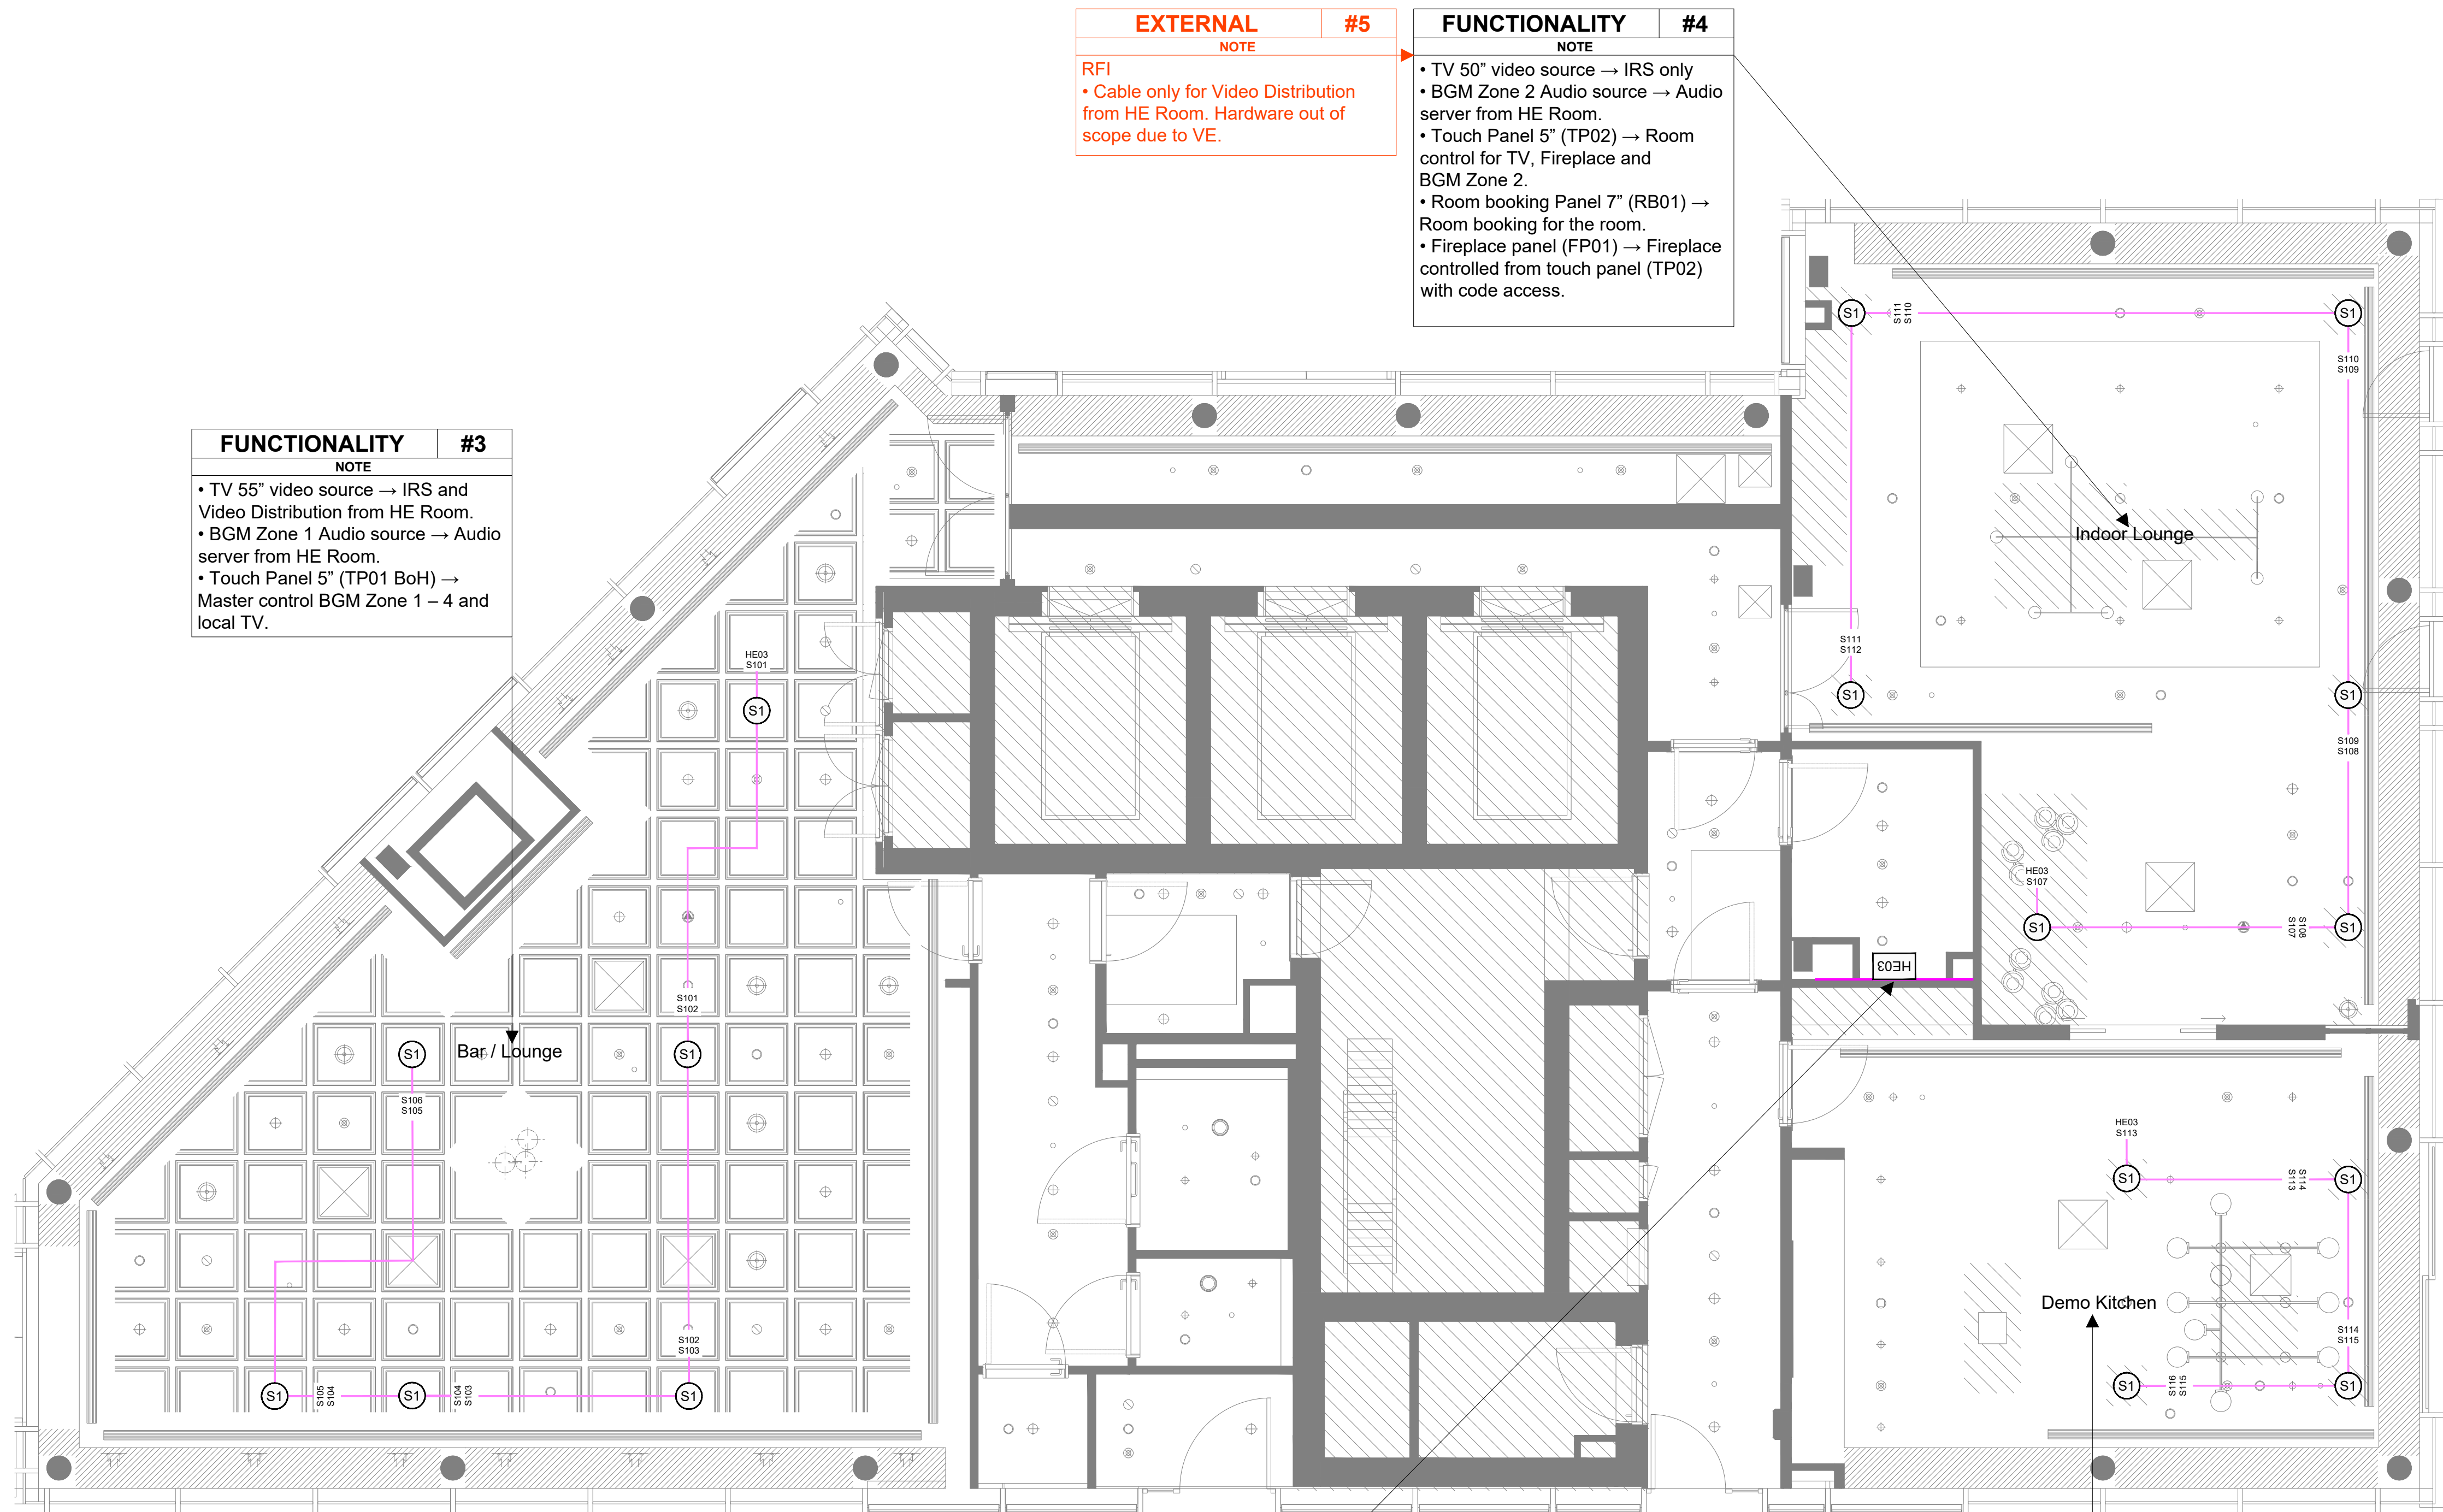

FUNCTIONALITY	#3
NOTE	
• TV 55" video source → IRS and Video Distribution from HE Room.	
• BGM Zone 1 Audio source → Audio server from HE Room.	
• Touch Panel 5" (TP01 BoH) → Master control BGM Zone 1 – 4 and local TV.	

EXTERNAL	#5
NOTE	
RFI	
• Cable only for Video Distribution from HE Room. Hardware out of scope due to VE.	

FUNCTIONALITY	#4
NOTE	
• TV 50" video source → IRS only	
• BGM Zone 2 Audio source → Audio server from HE Room.	
• Touch Panel 5" (TP02) → Room control for TV, Fireplace and BGM Zone 2.	
• Room booking Panel 7" (RB01) → Room booking for the room.	
• Fireplace panel (FP01) → Fireplace controlled from touch panel (TP02) with code access.	

EXTERNAL	#6
NOTE	
RFI	
• Confirm location, size and performance of FCU in the head end cupboard.	
• Confirm Fire alarm interface requirement for integration with AV - purpose of audio ducking.	
• Confirm Lighting Integration details (TH to confirm with Nomico).	

FUNCTIONALITY	#5
NOTE	
• Video Source → Sky (1 for internal and 1 for external).	
• Video Distribution → AV over network cable (1 for internal and 1 for external).	
• Audio Source → One Audio Server for both.	

FUNCTIONALITY	#6
NOTE	
• BGM Zone 3 Audio source → Audio server from HE Room.	
• Touch Panel 5" (TP03) → Room control for BGM Zone 3.	
• Room booking Panel 7" (RB02) → Room booking for the room.	

NOTES

Reference Drawings

17010_AAM_BD_17_DR_A_06461.P10.11 (RCP)

LEGEND

Item Example	
M1	"M1" Wall Mounted Media Plate 01
M102	"Cables" 2x CAT6A
HE01	"M1" Item ID "02" Unique Number
	"HE01" Head End
Head End Equipment	
HExx	Wall Rack
By Others	
• IRS Aerial Feed(s)	
• LV (230V) Power	
• Fire Alarm Interface(s)	
• HVAC Cooling	
• Landlords Network Connection(s)	
Wall Mounted Equipment	
M1	Media Plate 01
By Others	
• IRS Aerial Feed(s)	
• LV(230V) Power	
M6	Media Plate 06
RB	Room Booking Panel
TP	Touch Panel
FP	Fire Place
Speaker Types	
S1	Speaker Type 1 - Ceiling
S2	Speaker Type 2 - Wall Mount
S3	Speaker Type 3 - External
S4	Speaker Type 4 - External
S5	Speaker Type 5 - External Wall Mount
S6	Speaker Type 6 - External Wall Mount
S7	Speaker Type 7 - External Subwoofer
S8	Speaker Type 8 - Soundbar
Floorboxes	
FB	Floorbox
Cable Types	
	Speaker Cable
	TBC
	CAT6a Cable F/FTP
	Nexans [N100.692G-OC]
	WF100 Digital Coaxial Cable
	Webro [392100HCA]
	Cresnet Control Cable
	Cresnet [Cresnet-P-TL-SP1000]

For Construction

© Copyright. All rights to this drawing and its design are the property of SmartComm Ltd. Any use or duplication of this drawing is strictly prohibited without prior written permission of SmartComm Ltd.

Drawn By	SD	22/07/22	
Checked By	SK	22/07/22	
Issued By	BW	22/07/22	

SCALE NTS

PAGE SIZE A1



SmartComm Ltd Haffley Road Cressex Business Park High Wycombe Buckinghamshire HP12 3SN	Tel: +44 (0)1494 471 912 E-mail: info@smartcomm.co.uk Web: www.smartcomm.co.uk
---	--

C01	For Construction	22/07/22	SD
A02	For Approval	11/05/22	SD
A01	For Approval	29/06/21	CL
Rev	Description	Date	Name

Royal Mail Parkside
Block D Level 17
AV Layout - High level

Project	Section	Type	Number	Revision	Version
NEPS	BD-17	GA	11	C01	V03