


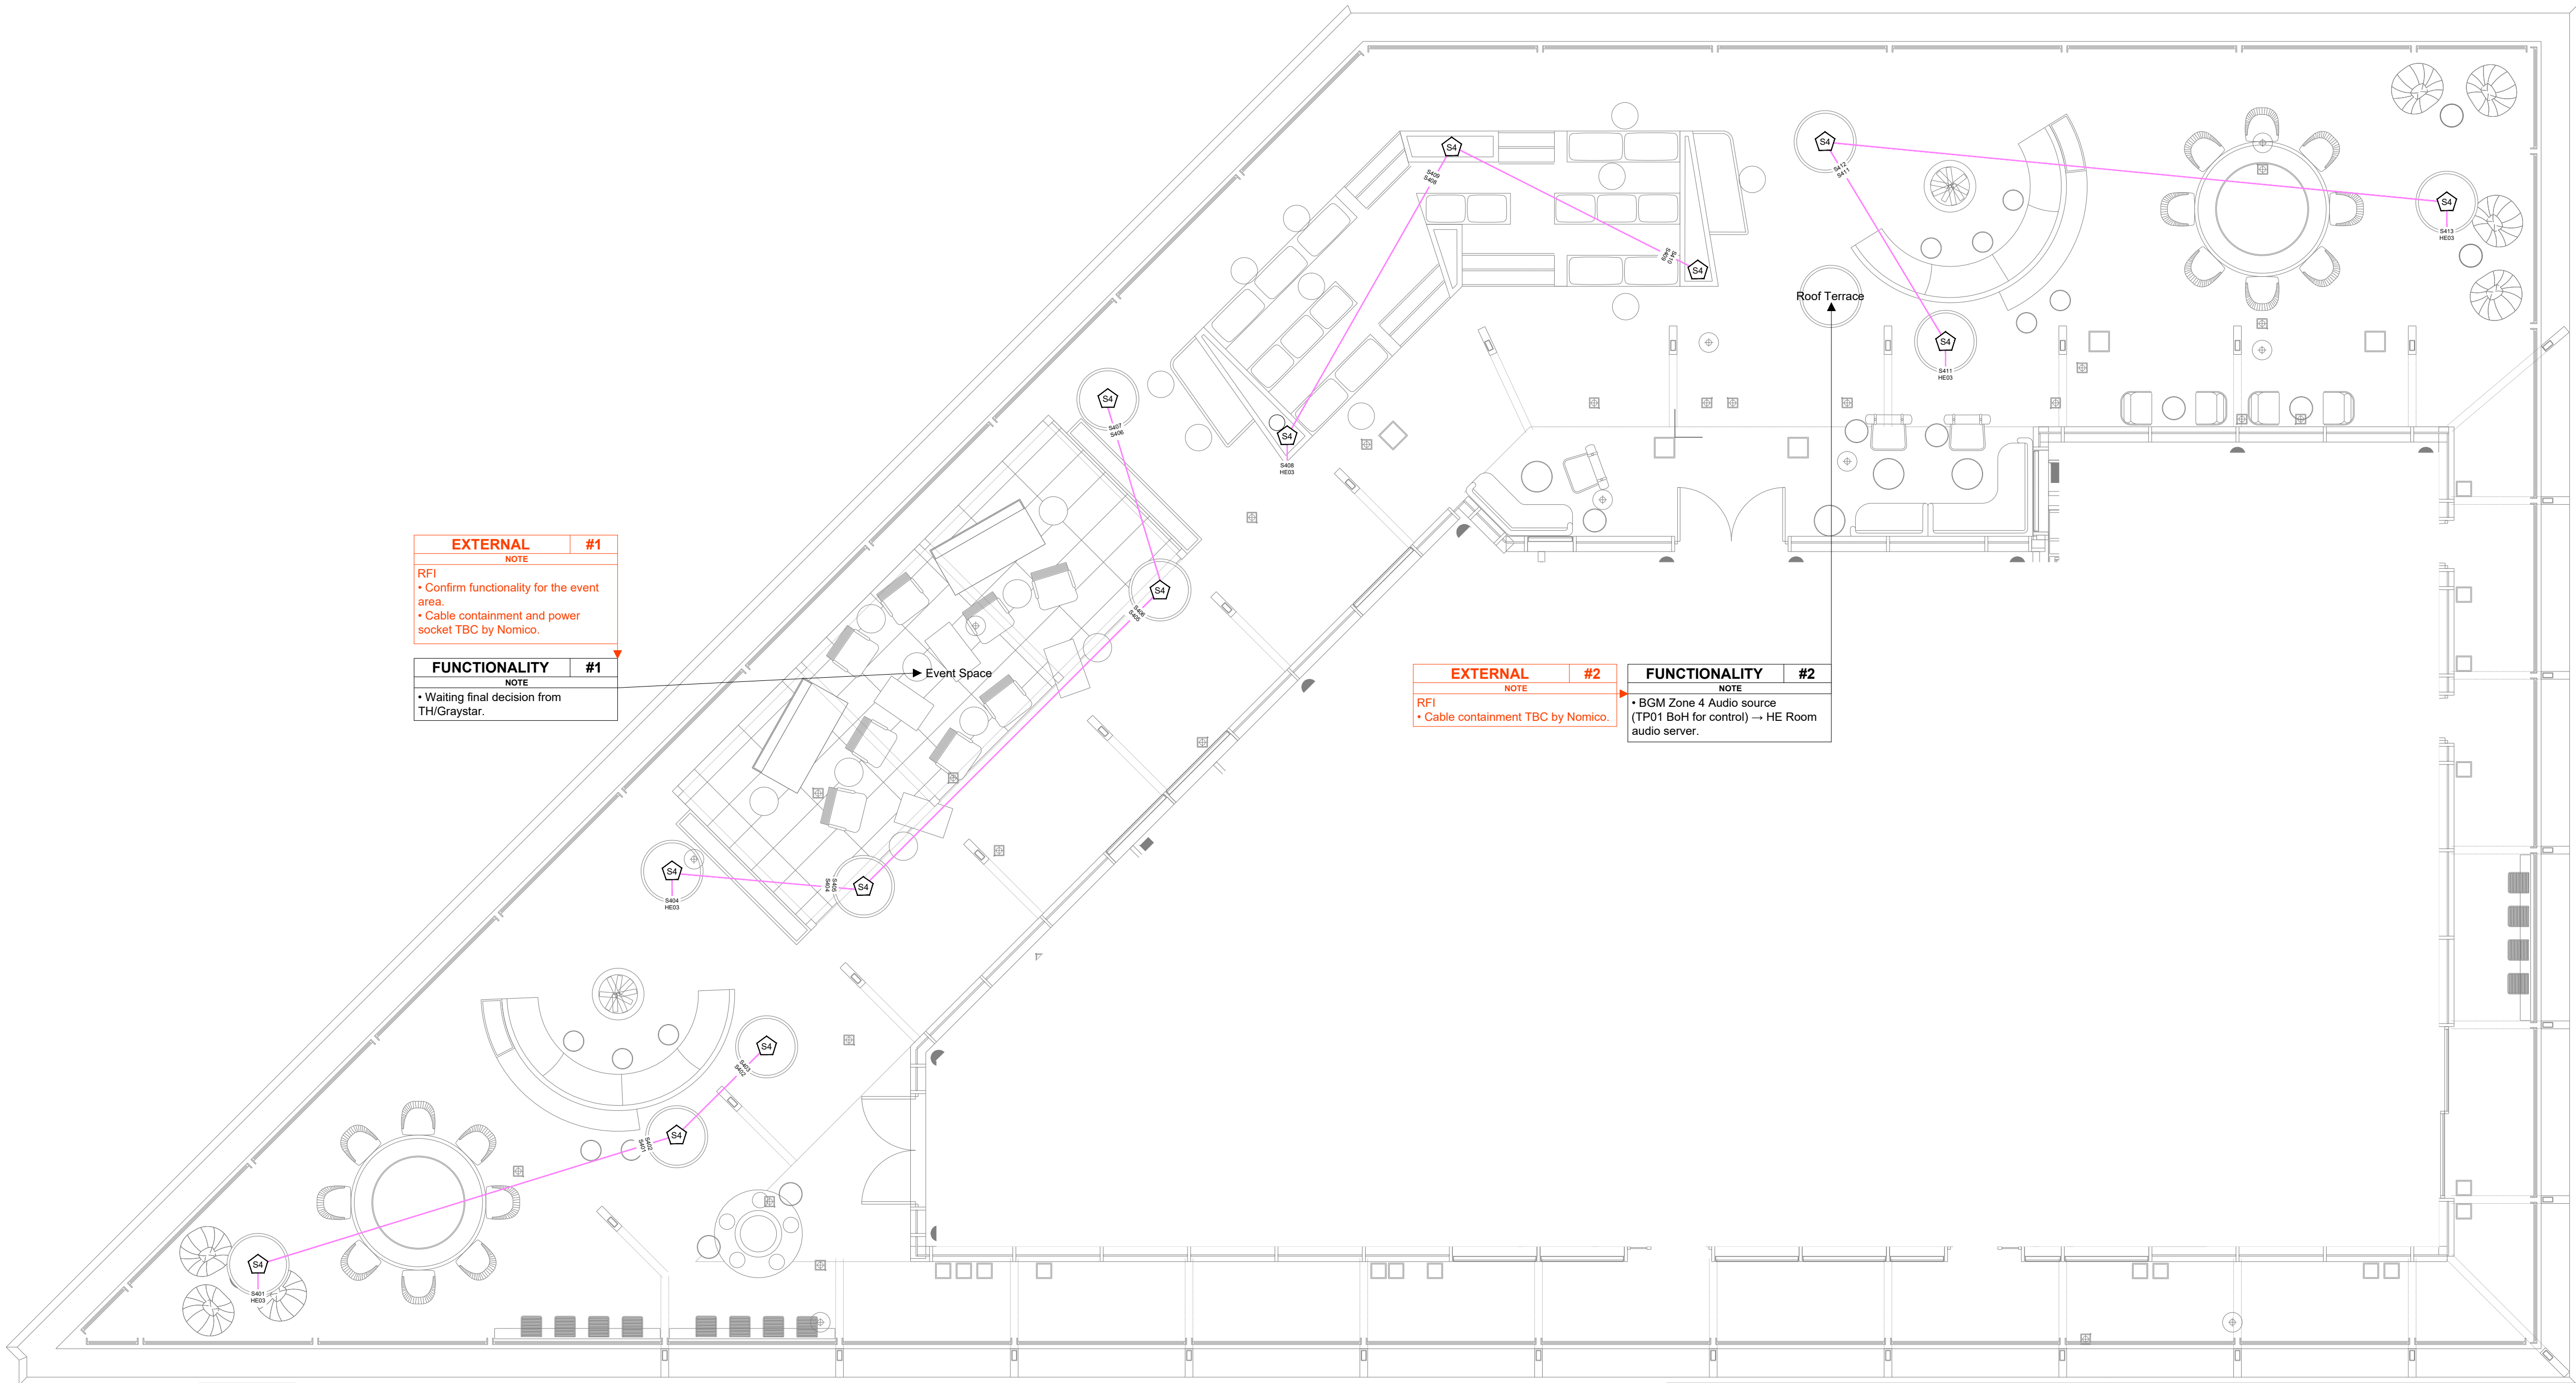

NOTES

Reference Drawings

GA_17010_AAM_BD_17_DR_A_06117.C10.15 (GA)

LEGEND

Item Example

M1 "M1" Wall Mounted Media Plate 01
M102 "Cables" 2x CAT6A
HE01 "M1" Item ID "02" Unique Number
"HE01" Head End

Head End Equipment

HExx

Wall Rack

By Others

- IRS Aerial Feed(s)
- LV (230V) Power
- Fire Alarm Interface(s)
- HVAC Cooling
- Landlords Network Connection(s)

Wall Mounted Equipment

M1

Media Plate 01

By Others

- IRS Aerial Feed(s)
- LV(230V) Power

M6

Media Plate 06

RB

Room Booking Panel

TP

Touch Panel

FP

Fire Place

Speaker Types

S1

Speaker Type 1 - Ceiling

S2

Speaker Type 2 - Wall Mount

S3

Speaker Type 3 - External

S4

Speaker Type 4 - External

S5

Speaker Type 5 - External Wall Mount

S6

Speaker Type 6 - External Wall Mount

S7

Speaker Type 7 - External Subwoofer

S8

Speaker Type 8 - Soundbar

Floorboxes

FB

Floorbox

Cable Types

- Speaker Cable
- TBC
- CAT6a Cable F/FTP
- Nexans [N100.692G-OC]
- WF100 Digital Coaxial Cable
- Webro [392 100HCA]
- Cresnet Control Cable
- Cresnet [Cresnet-P-TL-SP1000]

For Construction

© Copyright. All rights to this drawing and its design are the property of SmartComm Ltd. Any use or duplication of this drawing is strictly prohibited without prior written permission of SmartComm Ltd.

Drawn By	SD	22/07/22	
Checked By	SK	22/07/22	
Issued By	BW	22/07/22	

SCALE NTS

PAGE SIZE A1

smartcomm
integrating technology with vision

Smartcomm Ltd
Holford Road
Cressex Business Park
High Wycombe
Buckinghamshire
HP12 3SN
Tel: +44 (0)1494 471 912
E-mail: info@smartcomm.co.uk
Web: www.smartcomm.co.uk

C01	For Construction	22/07/22	SD
A04	For Approval	11/05/22	SD
A03	For Approval	31/08/21	SD
A02	For Approval	27/08/21	SD
A01	For Approval	29/07/21	CL
Rev	Description	Date	Name

Royal Mail Parkside
Block D Level 17 - Roof Terrace
AV Layout

Project	Section	Type	Number	Revision	Version
NEPS	BD-17	GA	31	C01	V05