


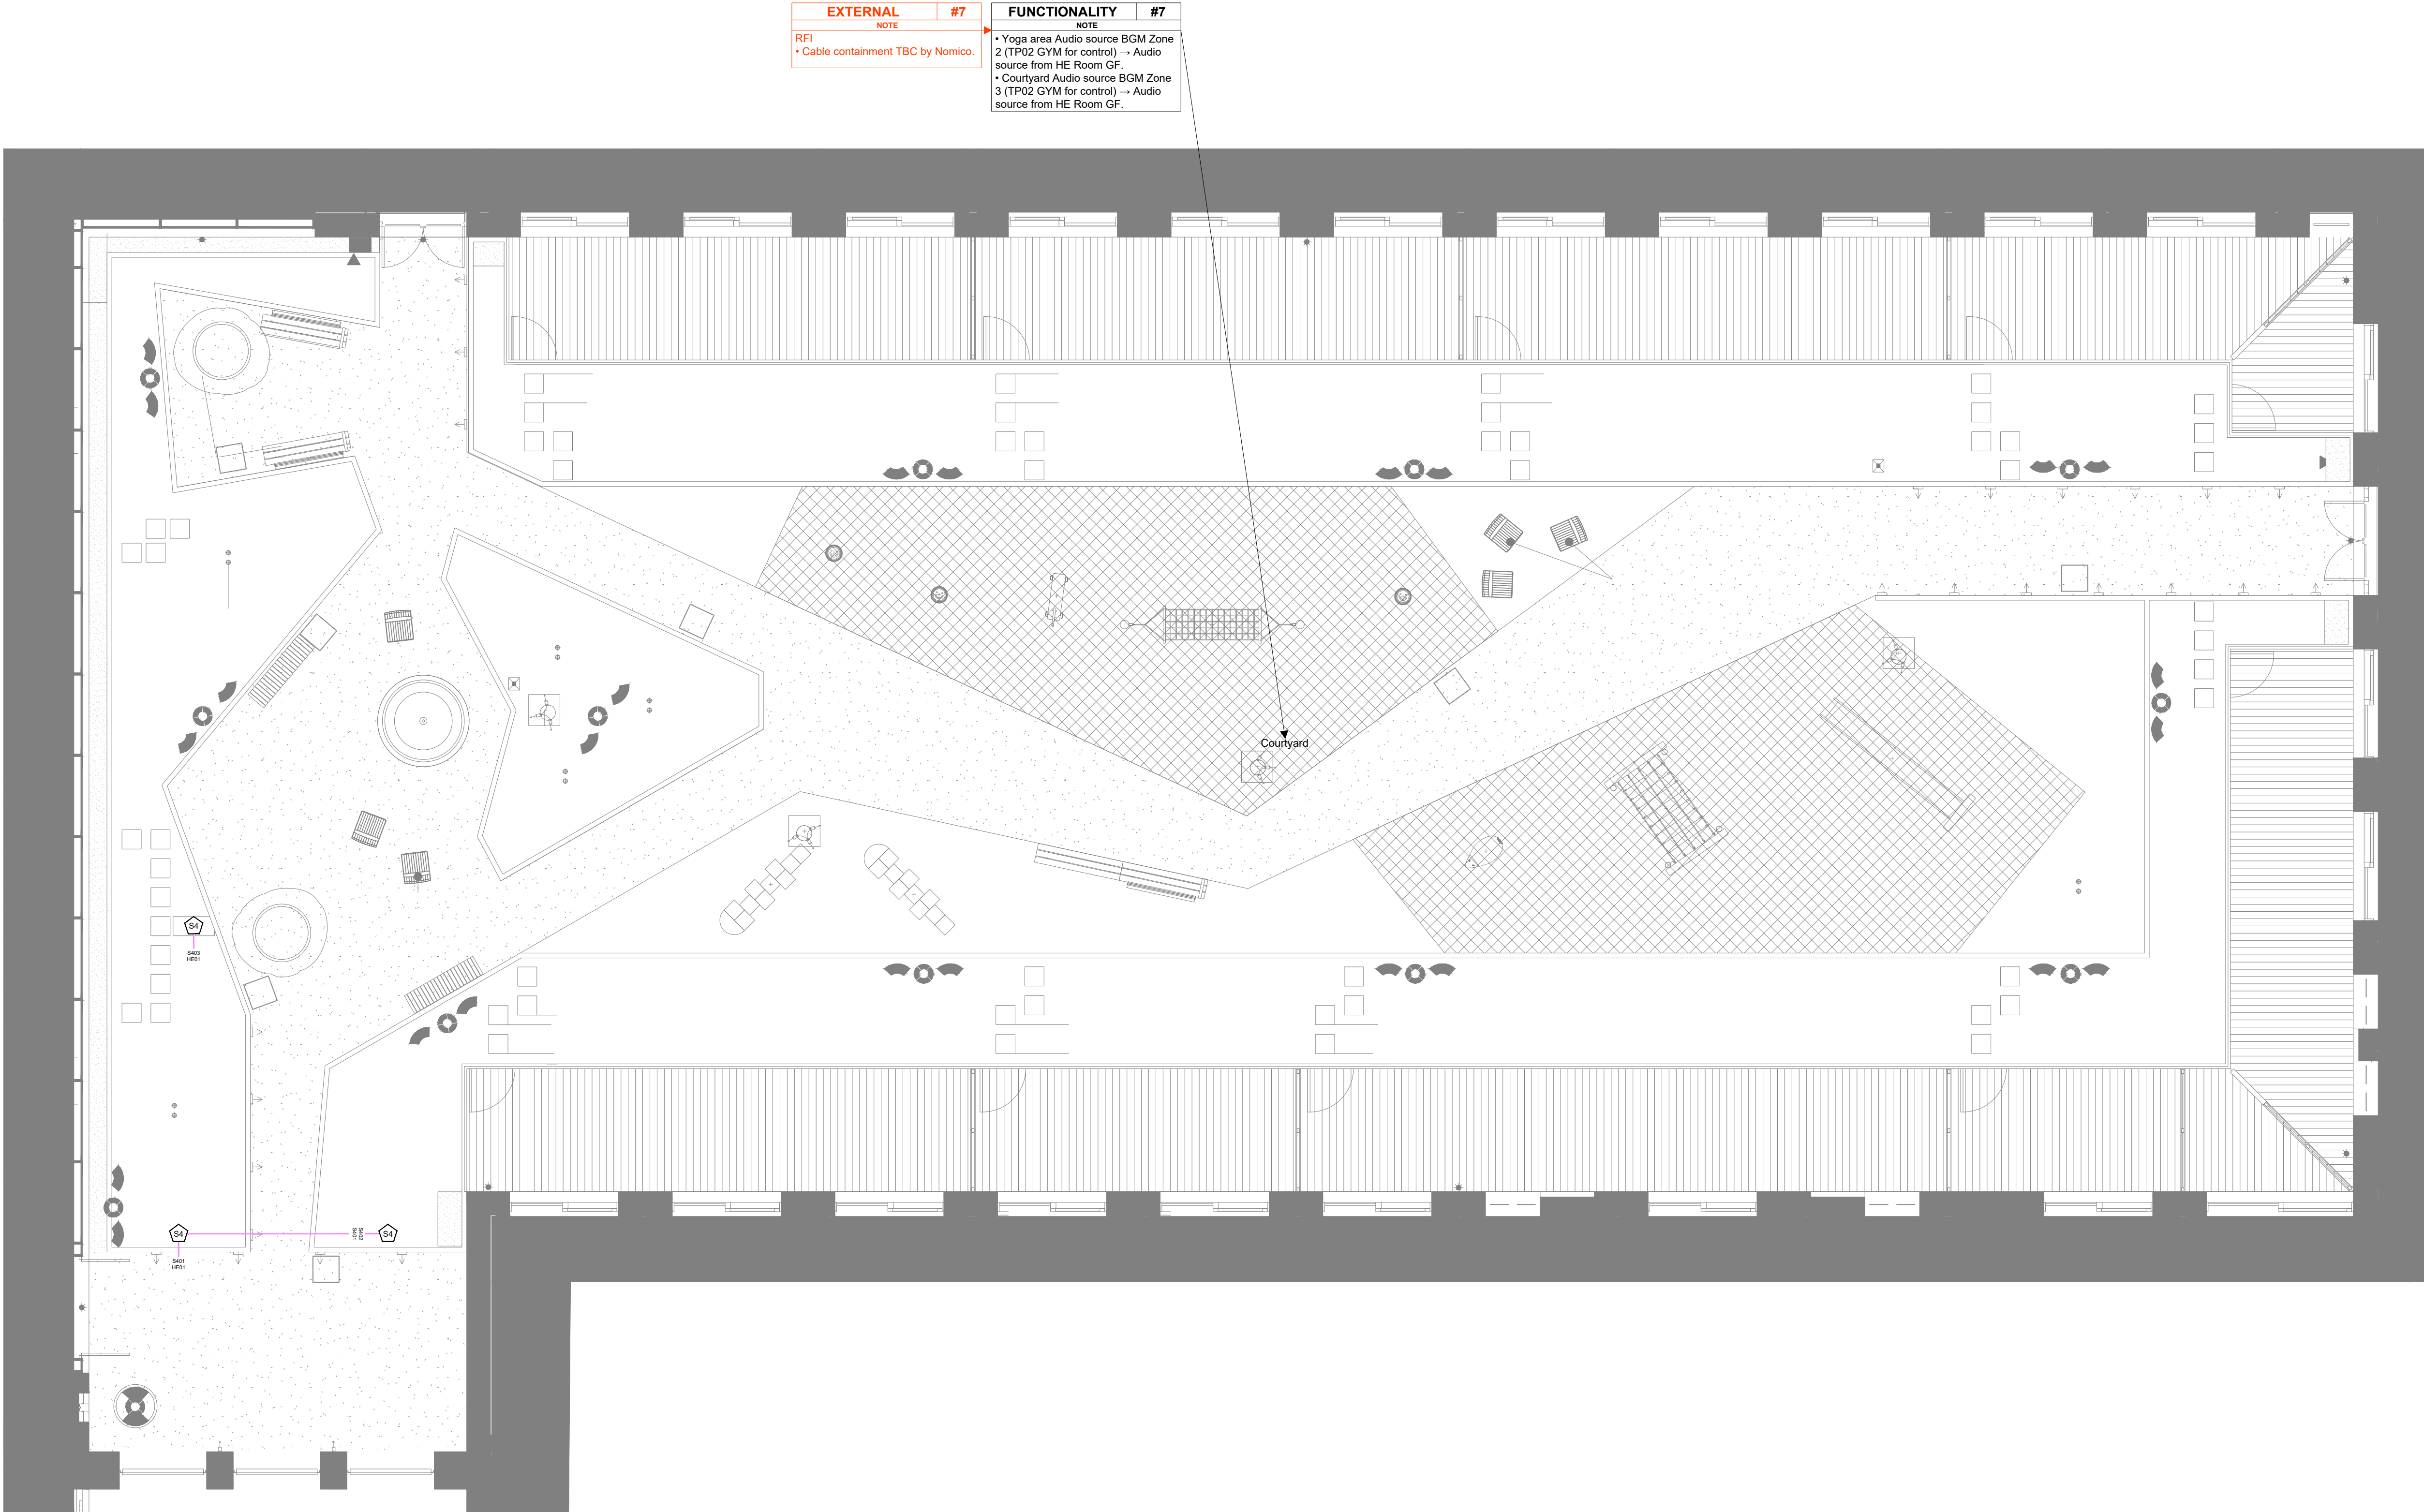

EXTERNAL	#7	FUNCTIONALITY	#7
NOTE		NOTE	
RFI		• Yoga area Audio source BGM Zone 2 (TP02 GYM for control) → Audio source from HE Room GF.	
• Cable containment TBC by Nomico.		• Courtyard Audio source BGM Zone 3 (TP02 GYM for control) → Audio source from HE Room GF.	

NOTES

Reference Drawings

17010_AAM_BD_01_DR_A_06420.C5.10 (GA)

LEGEND

Item Example

M1 "M1" Wall Mounted Media Plate 01
"Cables" 2x CAT6A
"M1" Item ID "02" Unique Number
"HE01" Head End

Head End Equipment

HExx Wall Rack
By Others
- IRS Aerial Feed(s)
- LV (230V) Power
- Fire Alarm Interface(s)
- HVAC Cooling
- Landlords Network Connection(s)

Wall Mounted Equipment

M1 Media Plate 01
By Others
- IRS Aerial Feed(s)
- LV(230V) Power
M6 Media Plate 06
RB Room Booking Panel
TP Touch Panel
FP Fire Place

Speaker Types

S1 Speaker Type 1 - Ceiling
S2 Speaker Type 2 - Wall Mount
S3 Speaker Type 3 - External
S4 Speaker Type 4 - External
S5 Speaker Type 5 - External Wall Mount
S6 Speaker Type 6 - External Wall Mount
S7 Speaker Type 7 - External Subwoofer
S8 Speaker Type 8 - Soundbar

Floorboxes

FB Floorbox

Cable Types

Speaker Cable
TBC
CAT6a Cable F/FTP
Nexans [N100.692G-OC]
WF100 Digital Coaxial Cable
Webro [392100HCA]
Cresnet Control Cable
Cresnet [Cresnet-P-TL-SP1000]

For Construction

© Copyright. All rights to this drawing and its design are the property of SmartComm Ltd. Any use or duplication of this drawing is strictly prohibited without prior written permission of SmartComm Ltd.

Drawn By	SD	06/05/2022
Checked By	SK	06/05/2022
Issued By	BW	06/05/2022

SCALE NTS

PAGE SIZE A1



Smartcomm Ltd
Holford Road
Cressex Business Park
High Wycombe
Buckinghamshire
HP12 3SN
Tel: +44 (0)1494 471 912
E-mail: info@smartcomm.co.uk
Web: www.smartcomm.co.uk

C01	For Construction	22/07/22	SD
A01	For Approval	06/05/22	SD
Rev	Description	Date	Name

Royal Mail Parkside
Block D Level 01 - Courtyard
AV Layout

Project	Section	Type	Number	Revision	Version
NEPS	BD-01	GA	31	C01	V03