


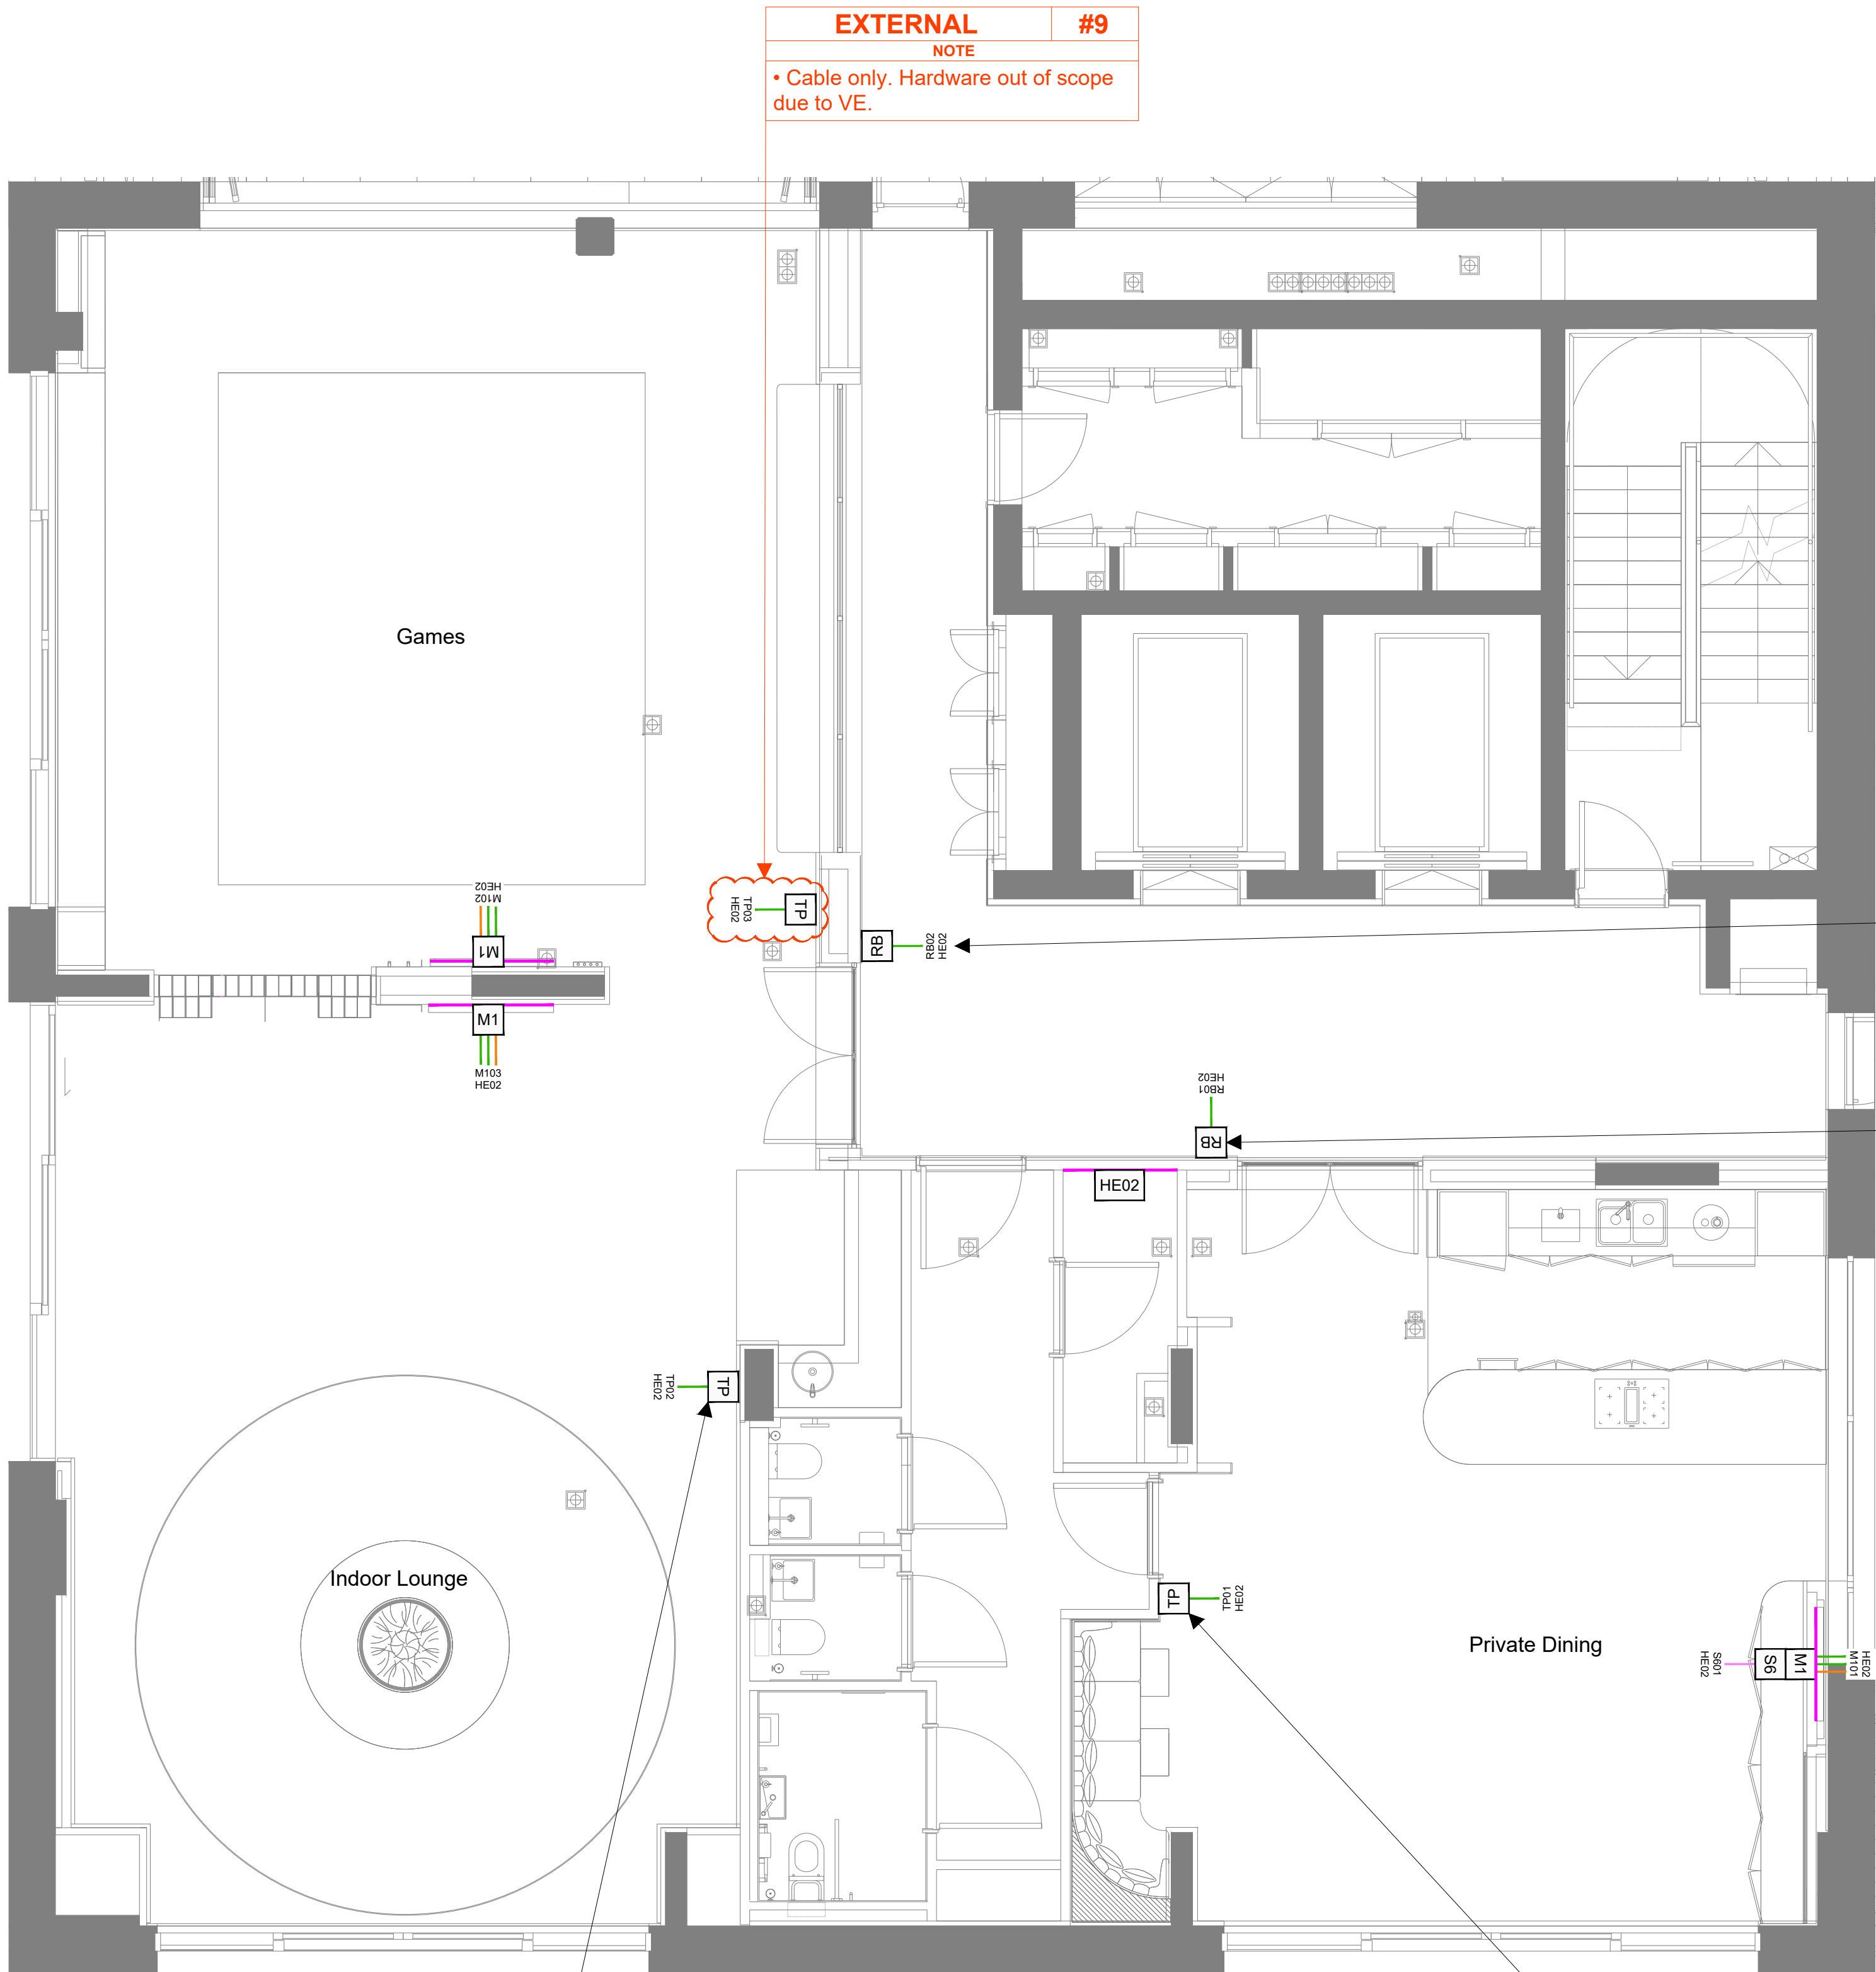

COORDINATION #5
NOTE
Touch panel setting out 1200mm
AFFL - Centres above Socket
Refer to RFI R001945

COORDINATION #6
NOTE
Touch panel setting out 1200mm
AFFL - Centered on wall
Refer to RFI R001945

COORDINATION #7
NOTE
Refer to RFI R001945

COORDINATION #8
NOTE
Room Booking Panel setting out
1300mm AFFL - Centres above
Socket
Refer to RFI R001945

EXTERNAL #9
NOTE
• Cable only. Hardware out of scope
due to VE.

NOTES

Reference Drawings

17010_AAM_BD_10_DR_A_06110.C12.16 (GA)

LEGEND

Item Example

M1 "M1" Wall Mounted Media Plate 01
"Cables" 2x CAT6A
"M1" Item ID "02" Unique Number
"HE01" Head End

Head End Equipment

HExx

Wall Rack

By Others

- IRS Aerial Feed(s)
- LV (230V) Power
- Fire Alarm Interface(s)
- HVAC Cooling
- Landlords Network Connection(s)

Wall Mounted Equipment

M1

Media Plate 01

By Others

- IRS Aerial Feed(s)
- LV(230V) Power

M6

Media Plate 06

RB

Room Booking Panel

TP

Touch Panel

FP

Fire Place

Speaker Types

S1

Speaker Type 1 - Ceiling

S2

Speaker Type 2 - Wall Mount

S3

Speaker Type 3 - External

S4

Speaker Type 4 - External

S5

Speaker Type 5 - External Wall Mount

S6

Speaker Type 6 - External Wall Mount

S7

Speaker Type 7 - External Subwoofer

S8

Speaker Type 8 - Soundbar

Floorboxes

FB

Floorbox

Cable Types

Speaker Cable

TBC

CAT6a Cable F/FTP

Nexans [N100.692G-OC]

WF100 Digital Coaxial Cable

Webro [392100HCA]

Cresnet Control Cable

Cresnet [Cresnet-P-TL-SP1000]

For Construction

© Copyright. All rights to this drawing and its design are the property of SmartComm Ltd. Any use or duplication of this drawing is strictly prohibited without prior written permission of SmartComm Ltd.

Drawn By	SD	22/07/22	
Checked By	SK	22/07/22	
Issued By	BW	22/07/22	

SCALE NTS

PAGE SIZE A1

smartcomm
integrating technology with vision

Smartcomm Ltd
Holford Road
Cressex Business Park
High Wycombe
Buckinghamshire
HP12 3SN
Tel: +44 (0)1494 471 912
E-mail: info@smartcomm.co.uk
Web: www.smartcomm.co.uk

Rev	Description	Date	Name
C01	For Construction	22/07/22	SD
A04	For Approval	10/05/22	SD
A03	For Approval	31/08/21	CL
A02	For Approval	29/07/21	CL
A01	For Approval	29/06/21	CL

Royal Mail Parkside
Block D Level 10
AV Layout - Low Level

Project	Section	Type	Number	Revision	Version
NEPS	BD-10	GA	01	C01	V05