


FUNCTIONALITY	#2
NOTE	
- Indoor Lounge TV 55" video source (M102) → IRS and Video Distribution from HE Room. - Indoor Lounge BGM Zone 1 Audio source → Audio server from HE Room. - Games Room TV 55" video source (M103) → IRS and Video Distribution from HE Room. - Games Room BGM Zone 2 Audio source → Audio server from HE Room. - Touch Panel 5" (TP02) → Room control for BGM Zone 1 and 2 and TVs. - Room booking Panel 7" (RB02) → Room booking for both rooms.	

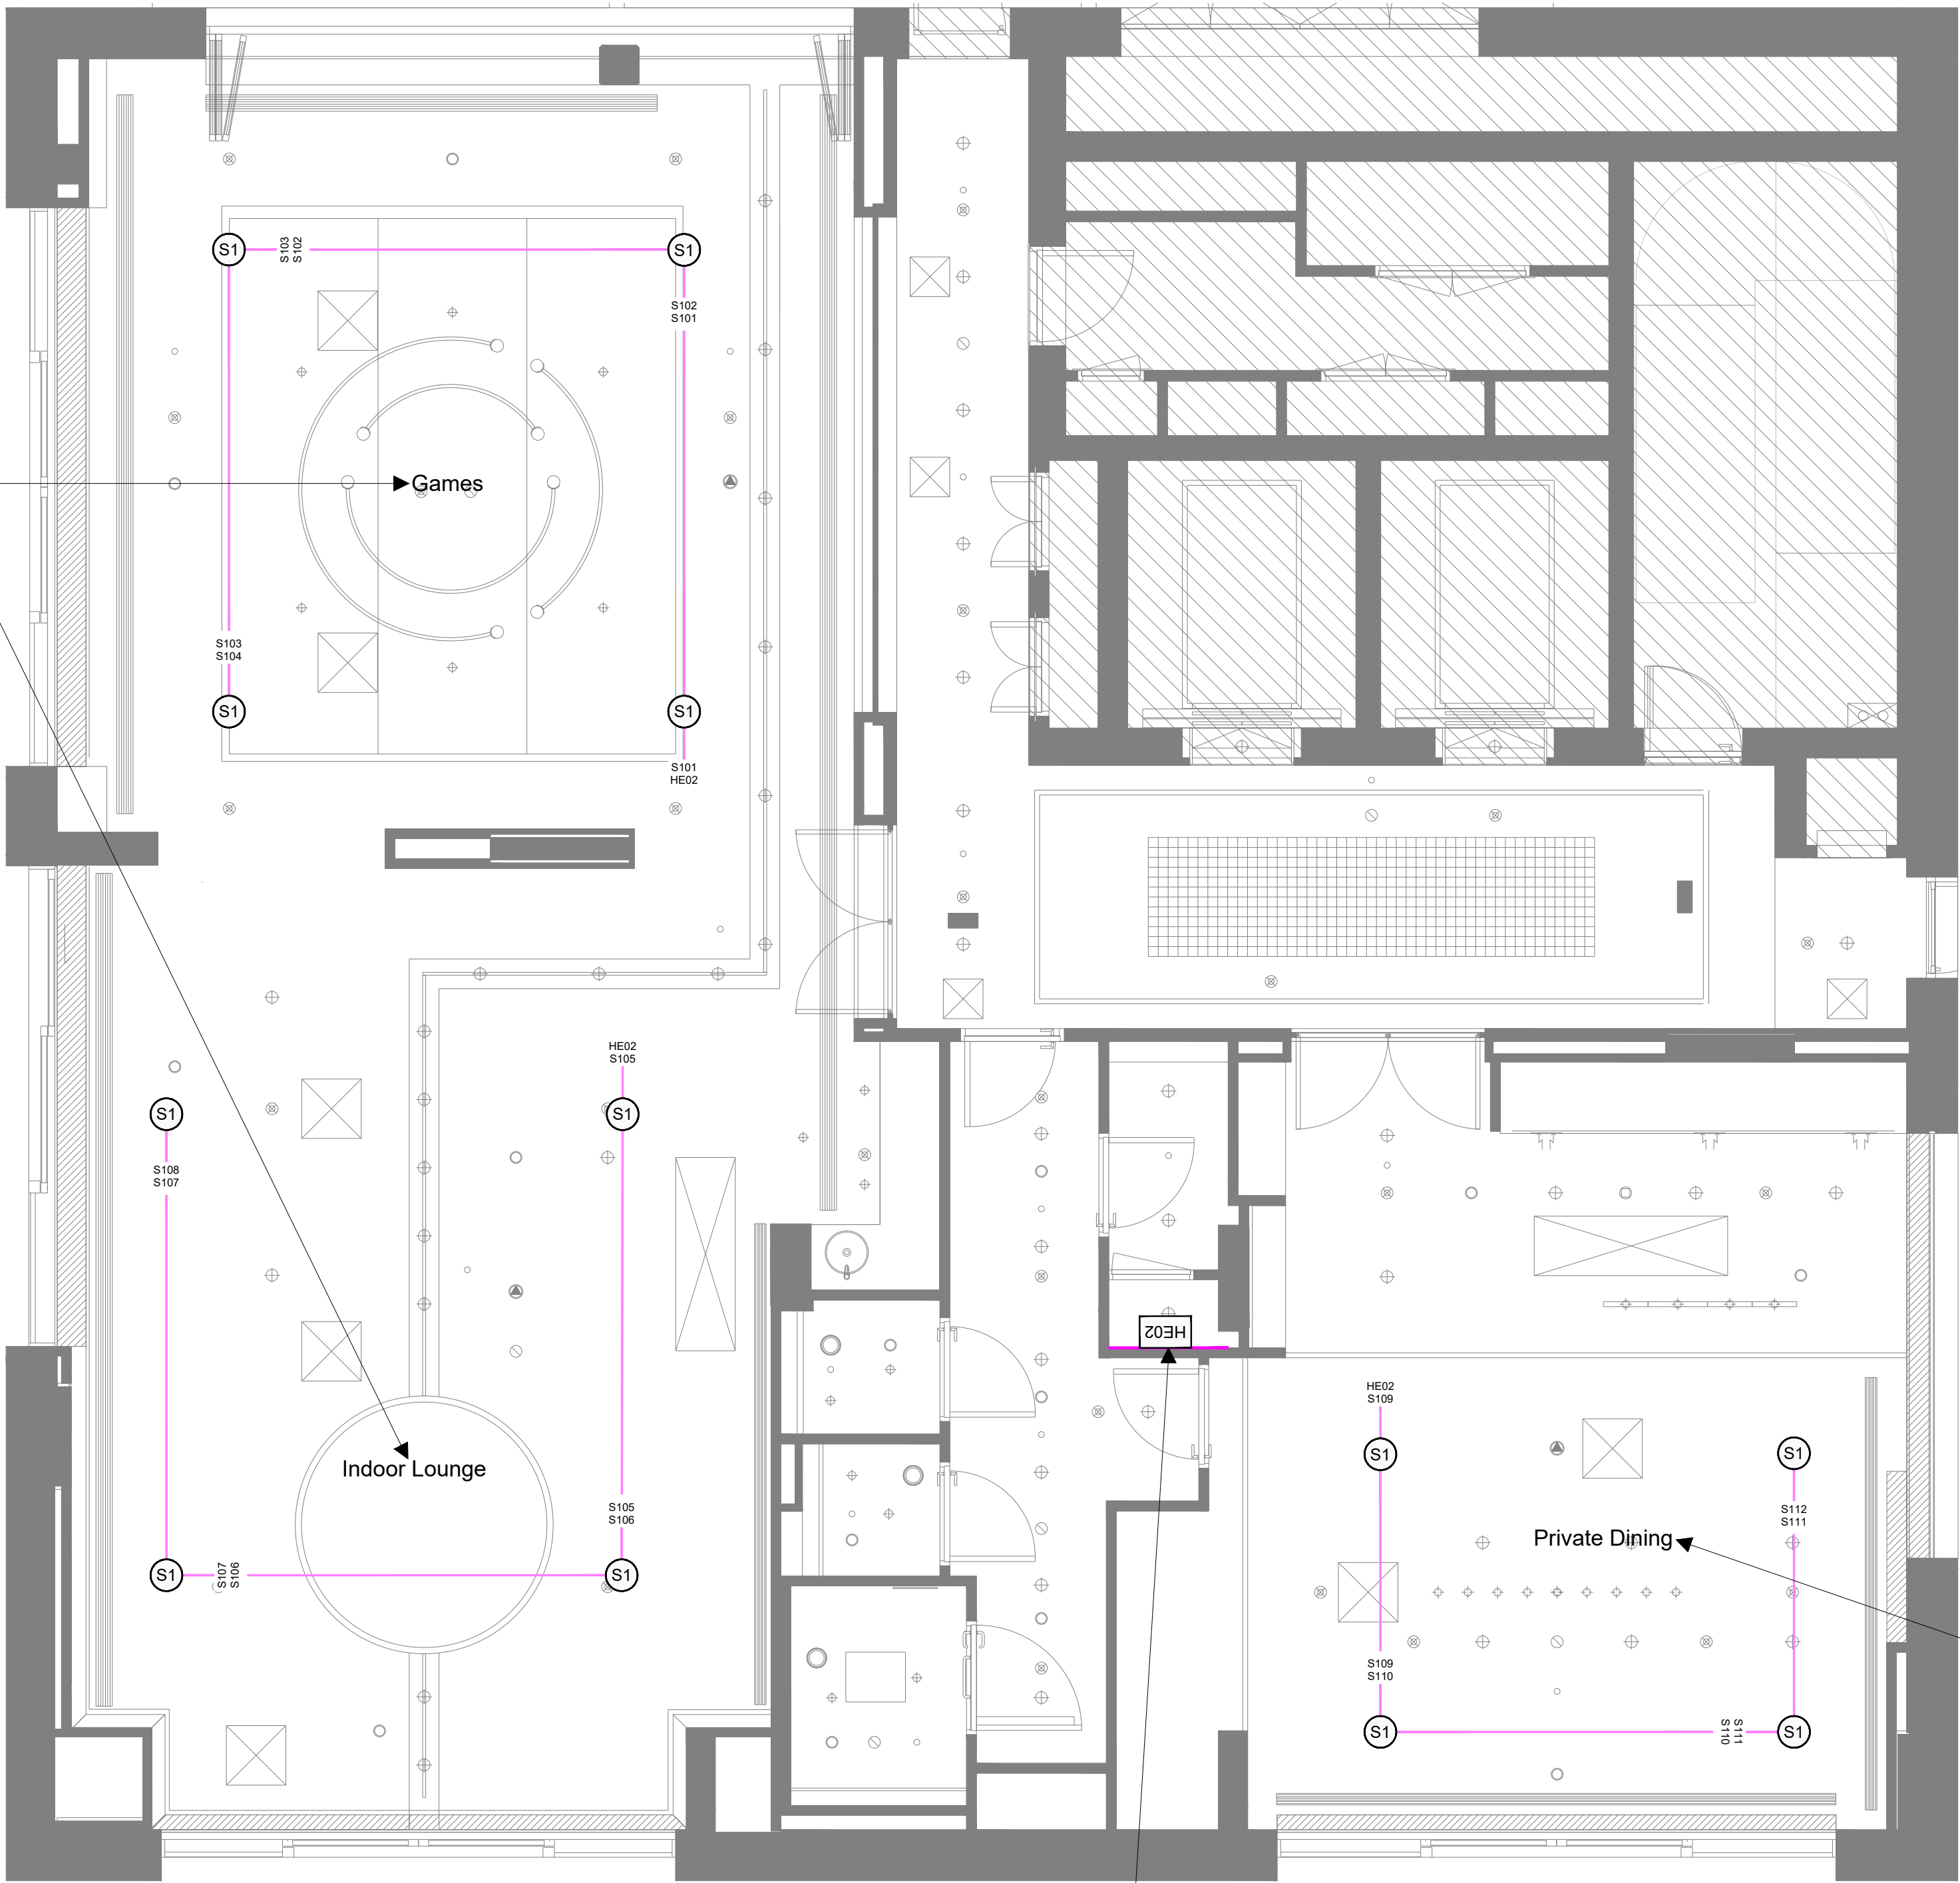

FUNCTIONALITY	#4
NOTE	
- TV 50" video source (M101) → IRS source only. - Soundbar (S601) → TV sound only. - BGM Zone 3 Audio source → Audio server from HE Room and local input visiting audio plug-in. - Touch Panel 5" (TP01) → Room control for BGM Zone 3 and TV. - Room booking Panel 7" (RB01) → Room booking for the room.	

EXTERNAL	#3
NOTE	
RFI - Confirm location, size and performance of FCU in the head end cupboard. - Confirm Fire alarm interface requirement for integration with AV - purpose of audio ducking. - Confirm Lighting Integration details (TH to confirm with Nomico).	

FUNCTIONALITY	#3
NOTE	
- Video Source → Sky. - Video Distribution → AV over network cable. - Audio Source → Audio Server.	

NOTES

Reference Drawings

17010_AAM_BD_10_DR_A_06445.P8.9 (RCP)

LEGEND

Item Example

M1	"M1" Wall Mounted Media Plate 01
M102	"Cables" 2x CAT6A
HE01	"M1" Item ID "02" Unique Number
	"HE01" Head End

Head End Equipment

HExx	Wall Rack
By Others	
- IRS Aerial Feed(s) - LV (230V) Power - Fire Alarm Interface(s) - HVAC Cooling - Landlords Network Connection(s)	

Wall Mounted Equipment

M1	Media Plate 01
By Others	
- IRS Aerial Feed(s) - LV(230V) Power	
M6	Media Plate 06
RB	Room Booking Panel
TP	Touch Panel
FP	Fire Place

Speaker Types

S1	Speaker Type 1 - Ceiling
S2	Speaker Type 2 - Wall Mount
S3	Speaker Type 3 - External
S4	Speaker Type 4 - External
S5	Speaker Type 5 - External Wall Mount
S6	Speaker Type 6 - External Wall Mount
S7	Speaker Type 7 - External Subwoofer
S8	Speaker Type 8 - Soundbar

Floorboxes

FB	Floorbox
----	----------

Cable Types

	Speaker Cable
	TBC
	CAT6a Cable F/FTP
	Nexans [N100.692G-OC]
	WF100 Digital Coaxial Cable
	Webro [392100HCAI]
	Cresnet Control Cable
	Cresnet [Cresnet-P-TL-SP1000]

For Construction

© Copyright. All rights to this drawing and its design are the property of SmartComm Ltd. Any use or duplication of this drawing is strictly prohibited without prior written permission of SmartComm Ltd.

Drawn By	SD	22/07/22	
Checked By	SK	22/07/22	
Issued By	BW	22/07/22	

SCALE NTS

PAGE SIZE A1



Smartcomm Ltd Haffley Road Cressle Business Park High Wycombe Buckinghamshire HP12 3SN	Tel: +44 (0)1494 471 912 E-mail: info@smartcomm.co.uk Web: www.smartcomm.co.uk
---	--

Rev	Description	Date	Name
C01	For Construction	22/07/22	SD
A03	For Approval	11/05/22	SD
A02	For Approval	26/08/21	CL
A01	For Approval	29/06/21	CL

Royal Mail Parkside
Block D Level 10
AV Layout - High Level

Project	Section	Type	Number	Revision	Version
NEPS	BD-10	GA	11	C01	V04