


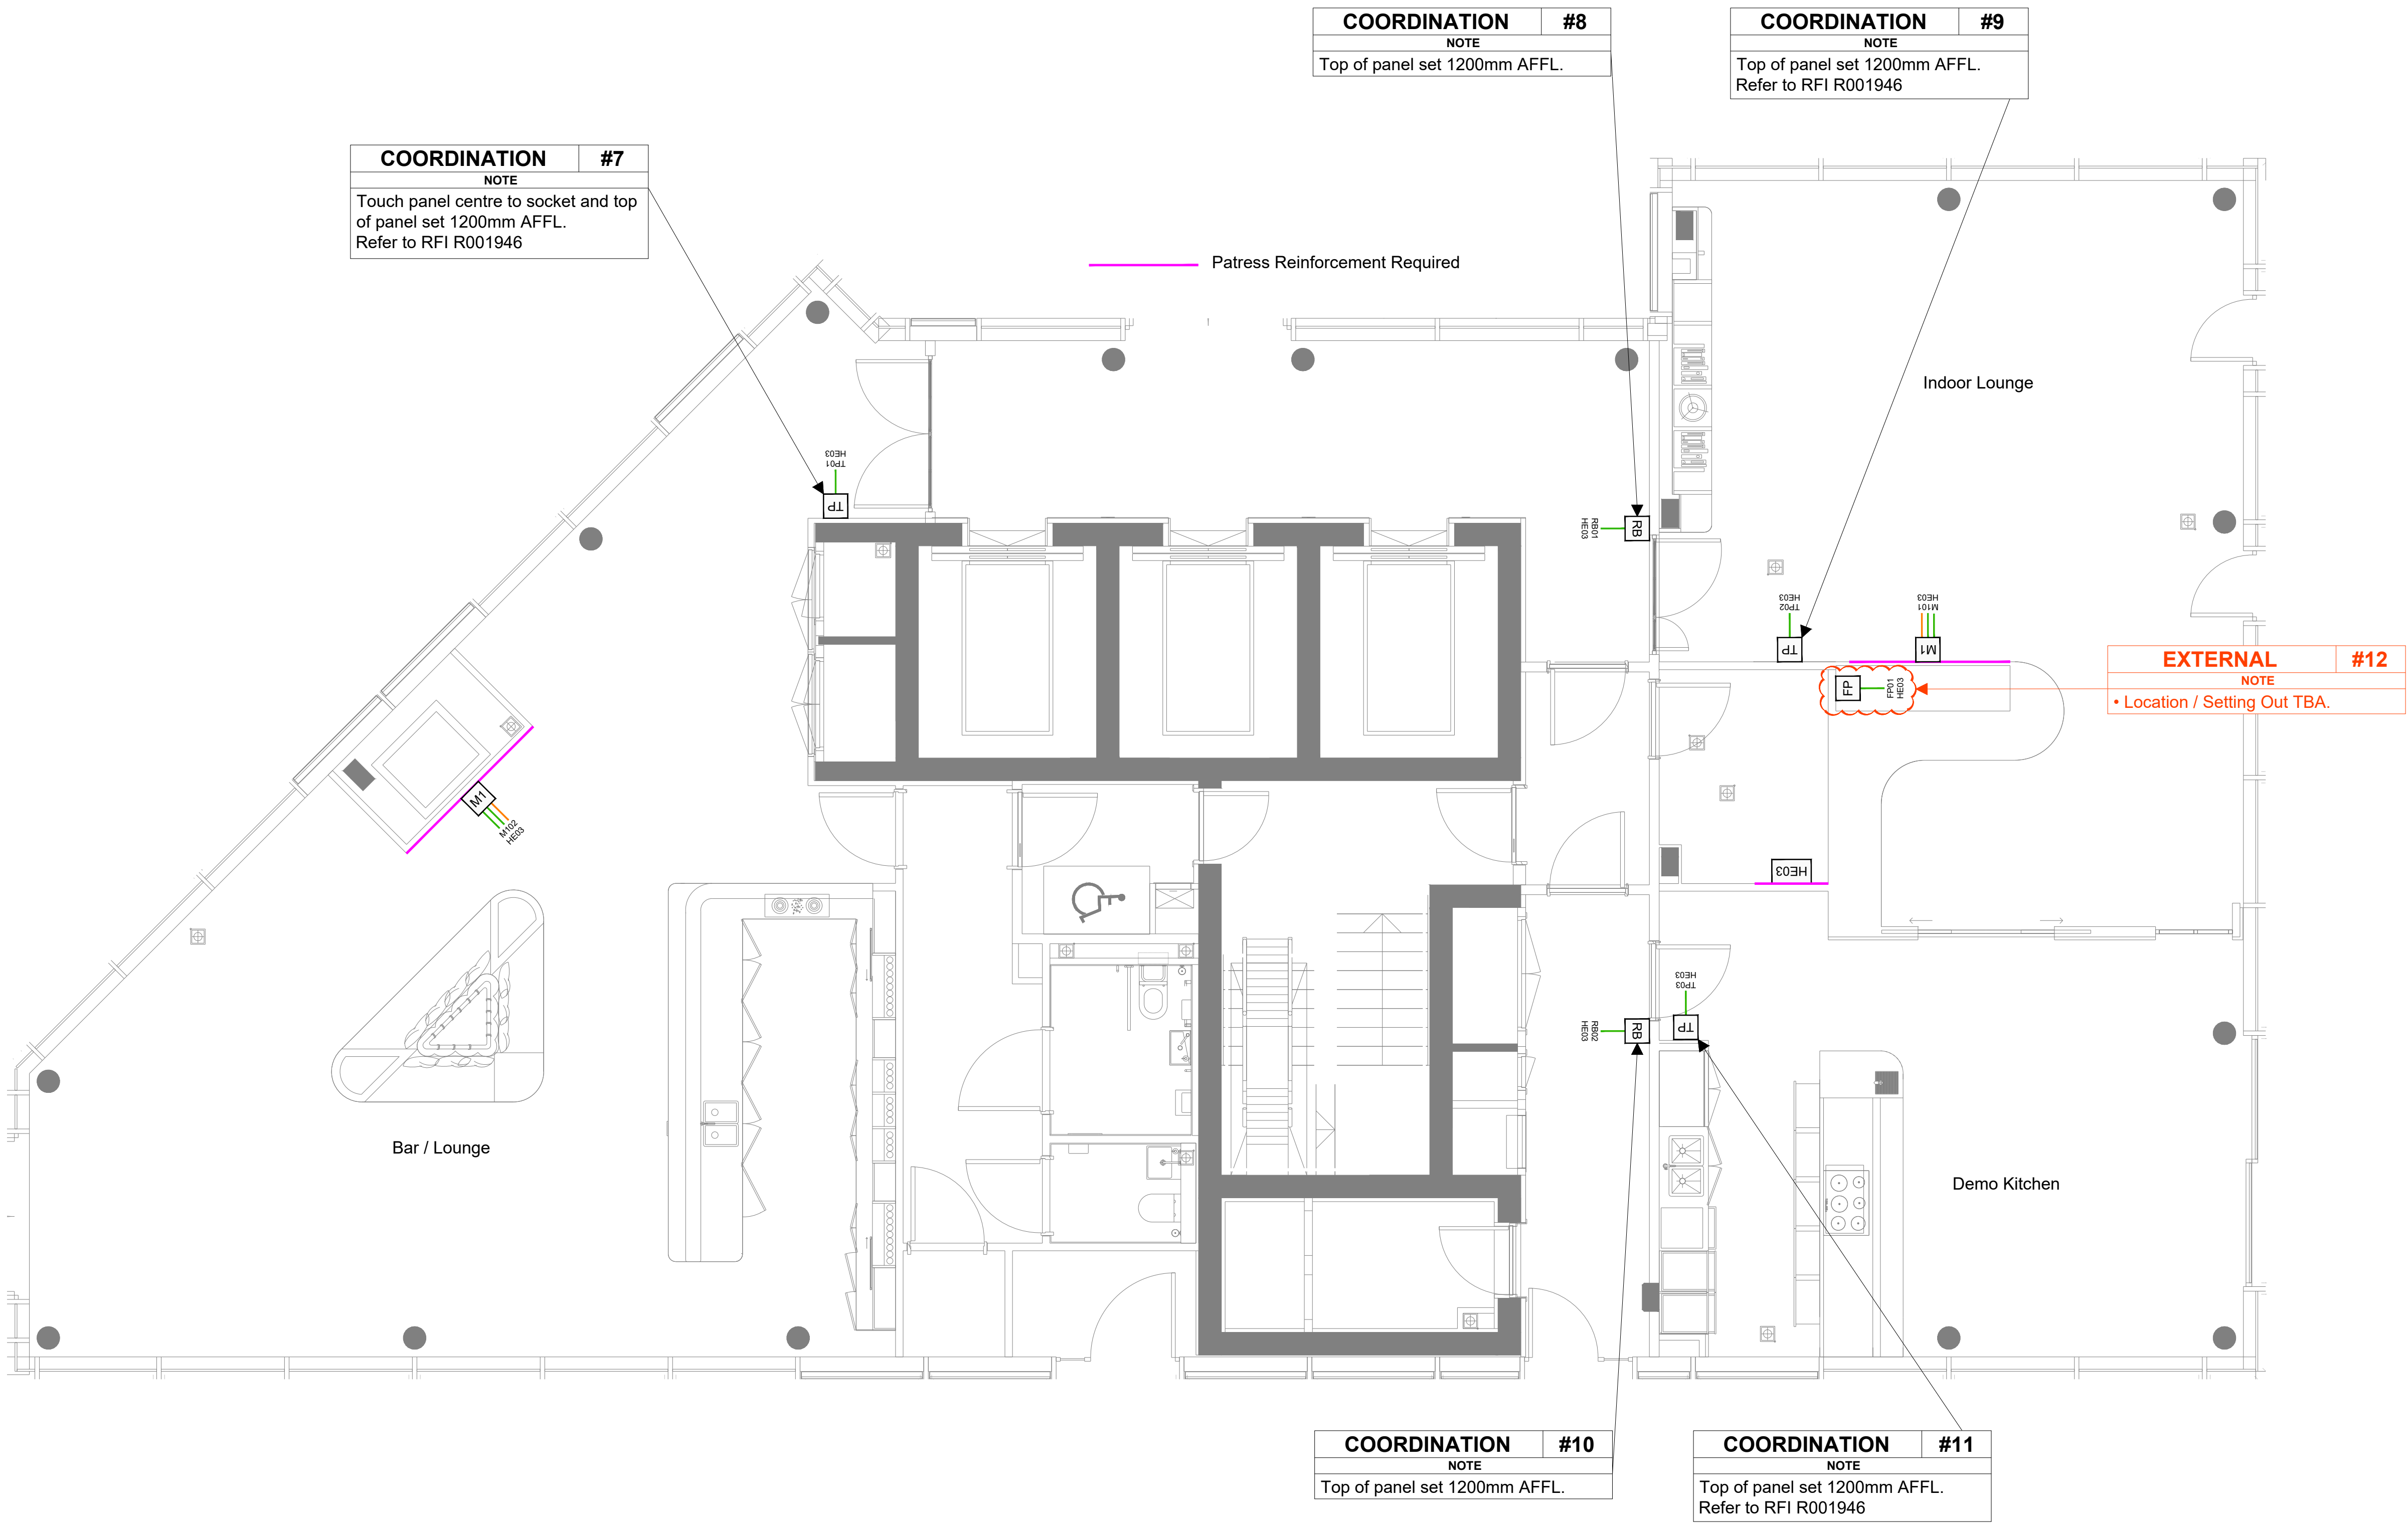

NOTES

Reference Drawings

17010_AAM_BD_17_DR_A_06117.C10.15 (GA)

TP Position based on RFI R001946

LEGEND

Item Example

M1 "M1" Wall Mounted Media Plate 01
"Cables" 2x CAT6a
"M1" Item ID "02" Unique Number
"HE01" Head End

Head End Equipment

HExx Wall Rack
By Others
- IRS Aerial Feed(s)
- LV (230V) Power
- Fire Alarm Interface(s)
- HVAC Cooling
- Landlords Network Connection(s)

Wall Mounted Equipment

M1 Media Plate 01
By Others
- IRS Aerial Feed(s)
- LV(230V) Power

M6 Media Plate 06

RB Room Booking Panel

TP Touch Panel

FP Fire Place

Speaker Types

S1 Speaker Type 1 - Ceiling
S2 Speaker Type 2 - Wall Mount
S3 Speaker Type 3 - External
S4 Speaker Type 4 - External
S5 Speaker Type 5 - External Wall Mount
S6 Speaker Type 6 - External Wall Mount
S7 Speaker Type 7 - External Subwoofer
S8 Speaker Type 8 - Soundbar

Floorboxes

FB Floorbox

Cable Types

Speaker Cable
TBC
CAT6a Cable F/FTP
Nexans [N100.692G-OC]
WF100 Digital Coaxial Cable
Webro [392 100HCA]
Cresnet Control Cable
Cresnet [Cresnet-P-TL-SP1000]

For Construction

© Copyright. All rights to this drawing and its design are the property of SmartComm Ltd. Any use or duplication of this drawing is strictly prohibited without prior written permission of SmartComm Ltd.

Drawn By	SD	22/07/22	
Checked By	SK	22/07/22	
Issued By	BW	22/07/22	

SCALE NTS

PAGE SIZE A1



Smartcomm Ltd
Haffley Road
Cresser Business Park
High Wycombe
Buckinghamshire
HP12 3SN

Tel: +44 (0)1494 471 912
E-mail: info@smartcomm.co.uk
Web: www.smartcomm.co.uk

Rev	Description	Date	Name
C01	For Construction	22/07/2022	SD
A03	For Approval	10/05/2022	SD
A02	For Approval	31/08/2021	CL
A01	For Approval	29/06/2021	CL

Royal Mail Parkside
Block D Level 17
AV Layout - Low Level

Project	Section	Type	Number	Revision	Version
NEPS	BD-17	GA	01	C01	V04