

NOTES

Reference Drawings

LEGEND

Item Example

M1 "M1" Wall Mounted Media Plate 01
"Cables" 2x CAT6A
"M1" Item ID "01" Unique Number
"HE01" Head End

Head End Equipment

HEXX Wall Rack
By Others
- IRS Aerial Feed(s)
- LV (230V) Power
- Fire Alarm Interface(s)
- HVAC Cooling
- Landlords Network Connection(s)

Wall Mounted Equipment

M1 Media Plate 01
By Others
- IRS Aerial Feed(s)
- LV(230V) Power

M6 Media Plate 06

RB Room Booking Panel

TP Touch Panel

FP Fire Place

Speaker Types

S1 Speaker Type 1 - Ceiling

S2 Speaker Type 2 - Wall Mount

S3 Speaker Type 3 - External

S4 Speaker Type 4 - External

S5 Speaker Type 5 - External Wall Mount

S6 Speaker Type 6 - External Wall Mount

S7 Speaker Type 7 - External Subwoofer

S8 Speaker Type 8 - Soundbar

Floorboxes

FB Floorbox

Cable Types

Speaker Cable
TBC
CAT6a Cable F/FTP
Nexans [N100.692G-OC]
WF100 Digital Coaxial Cable
Webro [392100HCA]
Cresnet Control Cable
Cresnet [Cresnet-P-TL-SP1000]

For Approval

© Copyright. All rights to this drawing and its design are the property of SmartComm Ltd. Any use or duplication of this drawing is strictly prohibited without prior written permission of SmartComm Ltd.

Drawn By SD 06/10/22
Checked By CL 07/10/22
Issued By BW 07/10/22

SCALE NTS
PAGE SIZE A1

smartcomm
integrating technology with vision

Smartcomm Ltd
Halfax Road
Cresnet Business Park
High Wycombe
Buckinghamshire
HP12 3JN
Tel: +44 (0)1494 471 912
E-mail: info@smartcomm.co.uk
Web: www.smartcomm.co.uk

A01 For Approval 06/10/22 SD
Rev Description Date Name

Royal Mail Parkside
Block D - Ground & First Floor
AV Schematic

Project Section Type Number Revision Version
NEPS BD-01 SC 01 A01 V03

LEVEL 1

GROUND FLOOR

NOTES

Reference Drawings

LEGEND

Item Example

M1 "M1" Wall Mounted Media Plate 01
"Cables" 2x CAT6A
"M1" Item ID "001" Unique Number
"HE01" Head End

Head End Equipment

HEXX Wall Rack
By Others
- IRS Aerial Feed(s)
- LV (230V) Power
- Fire Alarm Interface(s)
- HVAC Cooling
- Landor's Network Connection(s)

Wall Mounted Equipment

M1 Media Plate 01
By Others
- IRS Aerial Feed(s)
- LV(230V) Power

M6 Media Plate 06
RB Room Booking Panel
TP Touch Panel
FP Fire Place

Speaker Types

S1 Speaker Type 1 - Ceiling
S2 Speaker Type 2 - Wall Mount
S3 Speaker Type 3 - External
S4 Speaker Type 4 - External
S5 Speaker Type 5 - External Wall Mount
S6 Speaker Type 6 - External Wall Mount
S7 Speaker Type 7 - External Subwoofer
S8 Speaker Type 8 - Soundbar

Floorboxes

FB Floorbox

Cable Types

Speaker Cable
TBC
CAT6a Cable F/FTP
Nexans [N100.692G-OC]
WF100 Digital Coaxial Cable
Webro [392100HCAI]
Cresnet Control Cable
Cresstron [Cresnet-P-TL-SP1000]

For Approval

© Copyright. All rights to this drawing and its design are the property of SmartComm Ltd. Any use or duplication of this drawing is strictly prohibited without prior written permission of SmartComm Ltd.

Drawn By SD 06/10/22
Checked By CL 07/10/22
Issued By BW 07/10/22

SCALE NTS
PAGE SIZE A1

smartcomm
integrating technology with vision


Smartcomm Ltd
Halfax Road
Cresnet Business Park
High Wycombe
Buckinghamshire
HP12 3JN

Tel: +44 (0)1494 471 912
E-mail: info@smartcomm.co.uk
Web: www.smartcomm.uk

A01 For Approval 06/10/22 SD
Rev Description Date Name

Royal Mail Parkside
Block D Level 10
AV Schematic

Project	Section	Type	Number	Revision	Version
NEPS	BD-10	SC	01	A01	V01

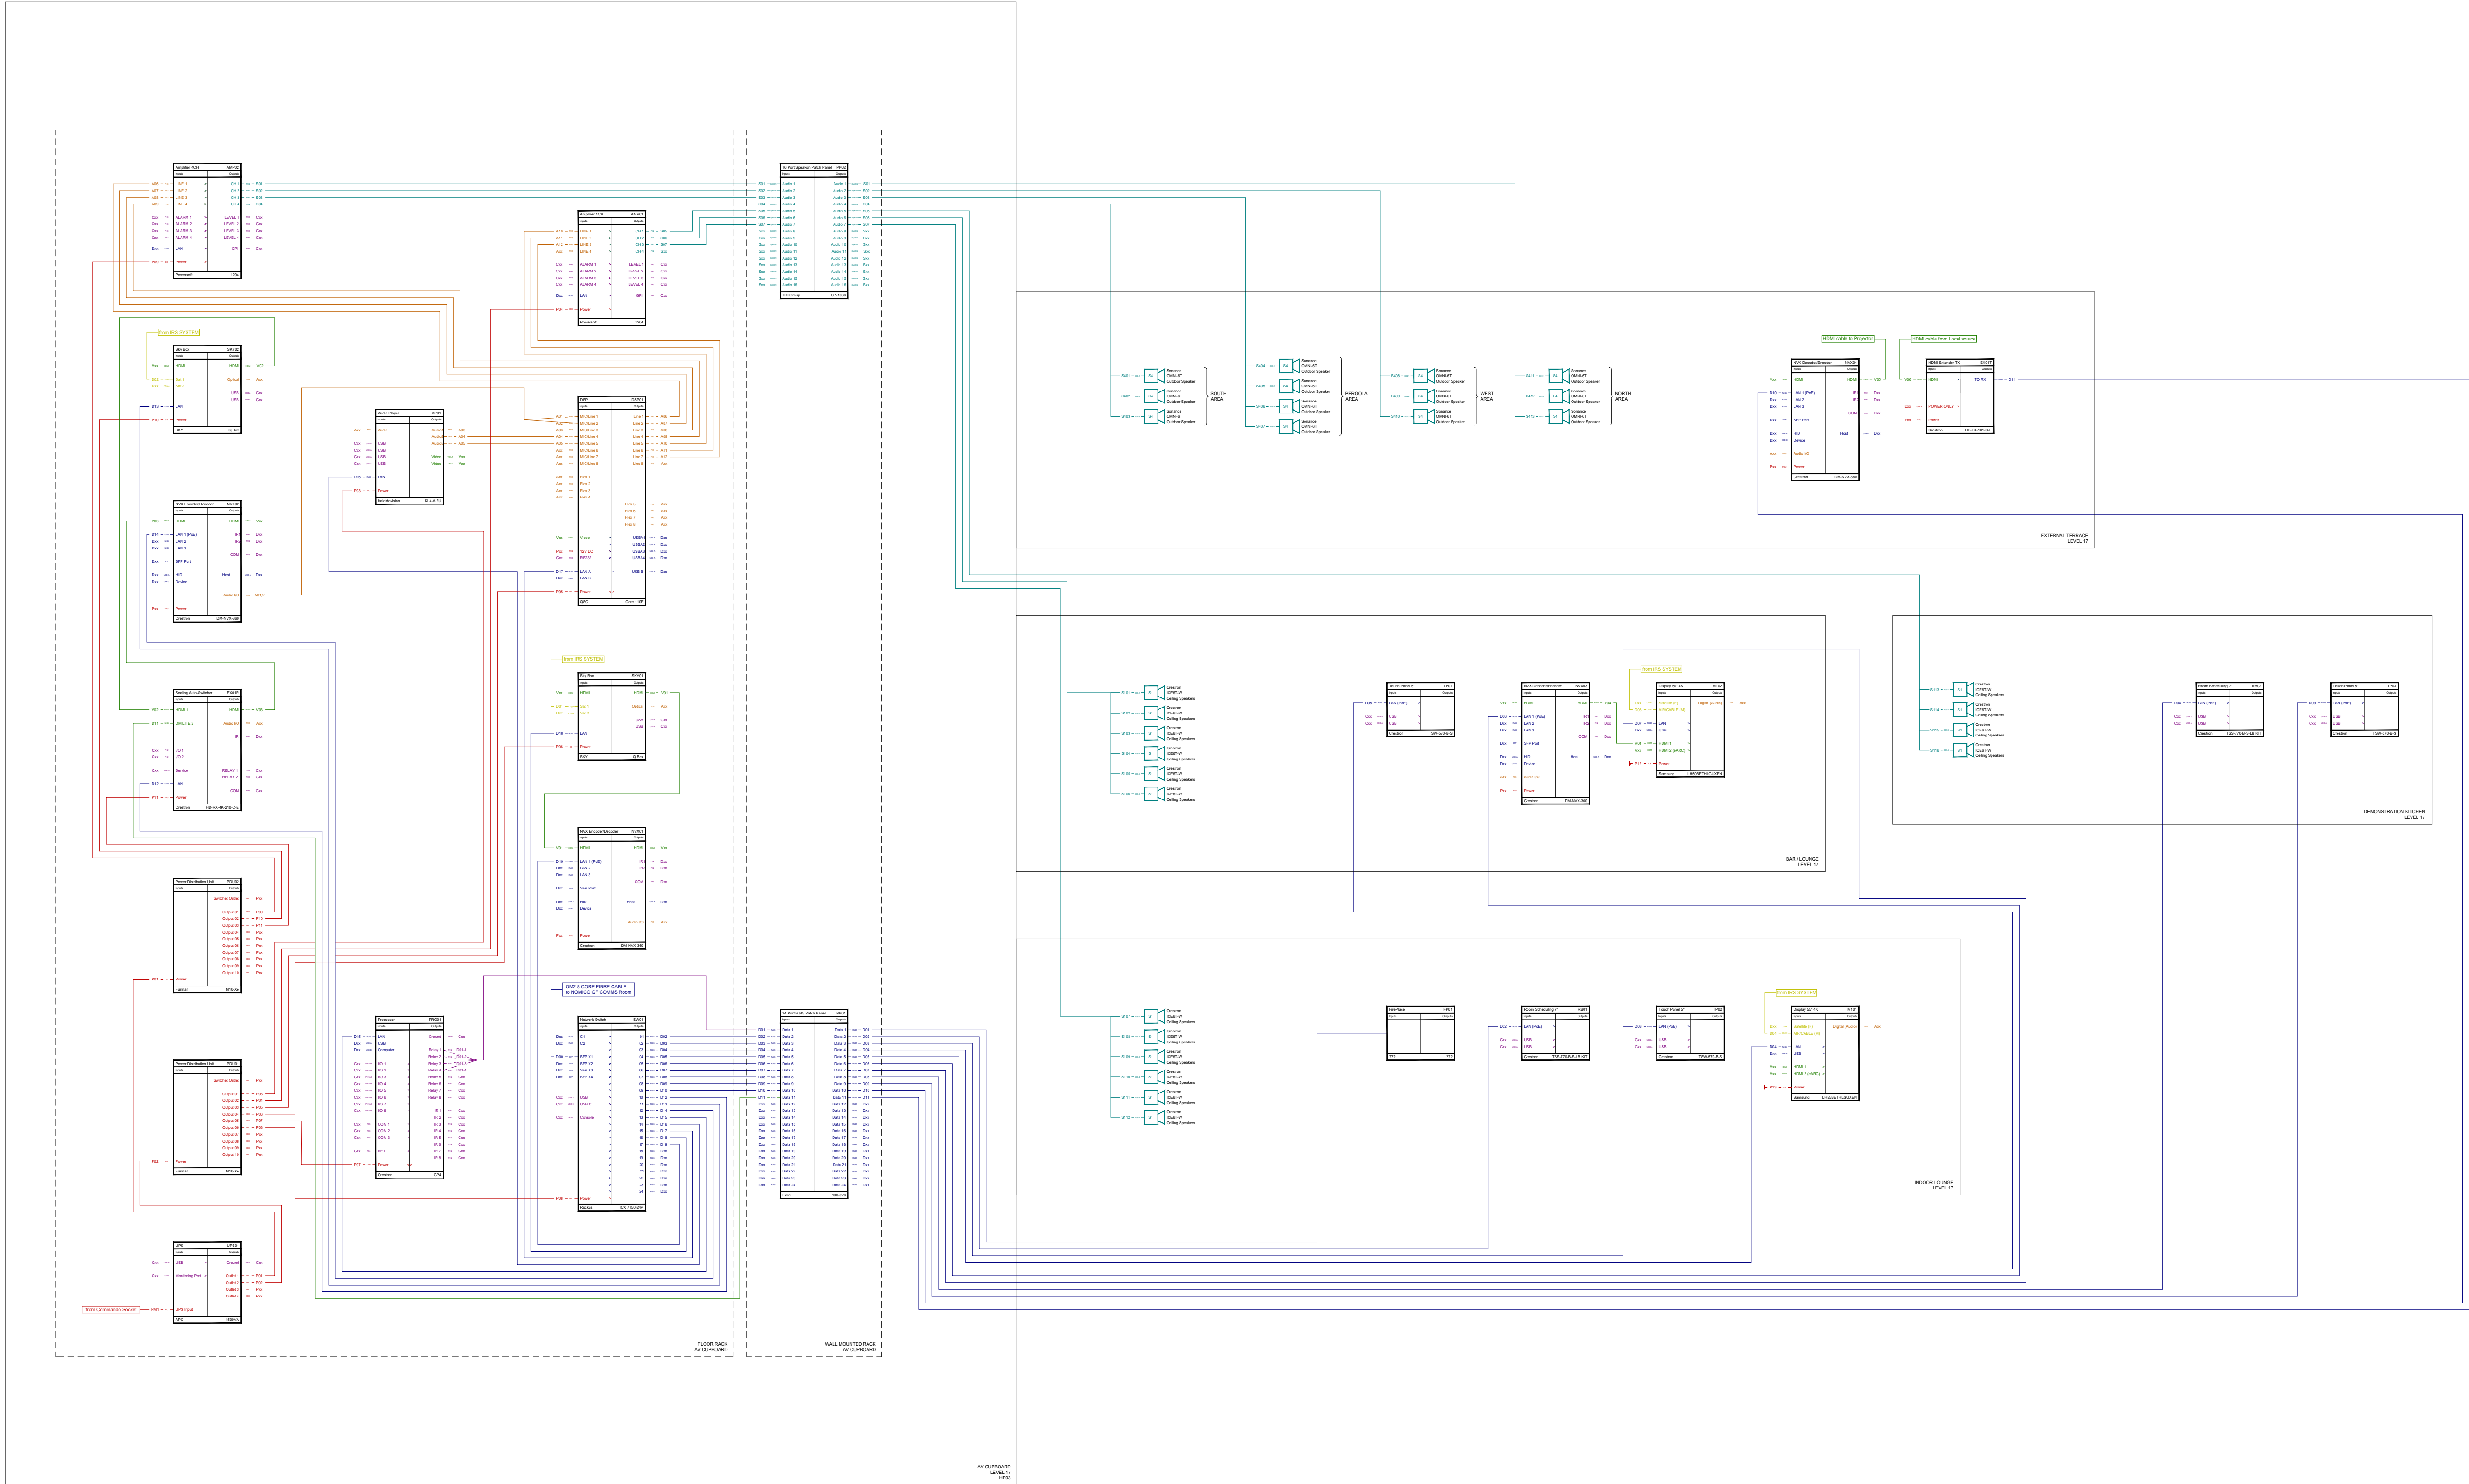

NOTES

Reference Drawings

LEGEND

Item Example

M1 "M1" Wall Mounted Media Plate 01
"Cables" 2x CAT6A
"M1" Item ID "02" Unique Number
"HE01" Head End

Head End Equipment

HEXX Wall Rack
By Others
- IRS Aerial Feed(s)
- LV (230V) Power
- Fire Alarm Interface(s)
- HVAC Cooling
- Landlord's Network Connection(s)

Wall Mounted Equipment

M1 Media Plate 01
By Others
- IRS Aerial Feed(s)
- LV(230V) Power

M6 Media Plate 06

RB Room Booking Panel

TP Touch Panel

FP Fire Place

Speaker Types

S1 Speaker Type 1 - Ceiling

S2 Speaker Type 2 - Wall Mount

S3 Speaker Type 3 - External

S4 Speaker Type 4 - External

S5 Speaker Type 5 - External Wall Mount

S6 Speaker Type 6 - External Wall Mount

S7 Speaker Type 7 - External Subwoofer

S8 Speaker Type 8 - Soundbar

Floorboxes

FB Floorbox

Cable Types

Speaker Cable
TBC

CAT6a Cable F/FTP
Nexans [N100.692G-OC]

WF100 Digital Coaxial Cable
Webro [392100HCA]

Cresnet Control Cable
Cresnet [Cresnet-P-TL-SP1000]

For Approval

© Copyright. All rights to this drawing and its design are the property of SmartComm Ltd. Any use or duplication of this drawing is strictly prohibited without prior written permission of SmartComm Ltd.

Drawn By	SD	06/10/22
Checked By	CL	07/10/22
Issued By	BW	07/10/22

SCALE NTS
PAGE SIZE A1

smartcomm
integrating technology with vision

Smartcomm Ltd
Halfax Road
Cresnet Business Park
High Wycombe
Buckinghamshire
HP12 3JN

Tel: +44 (0)1494 471 912
E-mail: info@smartcomm.co.uk
Web: www.smartcomm.co.uk

A01	For Approval	06/10/22	SD
Rev	Description	Date	Name

Royal Mail Parkside
Block D Level 17
AV Schematic

Project	Section	Type	Number	Revision	Version
NEPS	BD-17	SC	01	A01	V01