


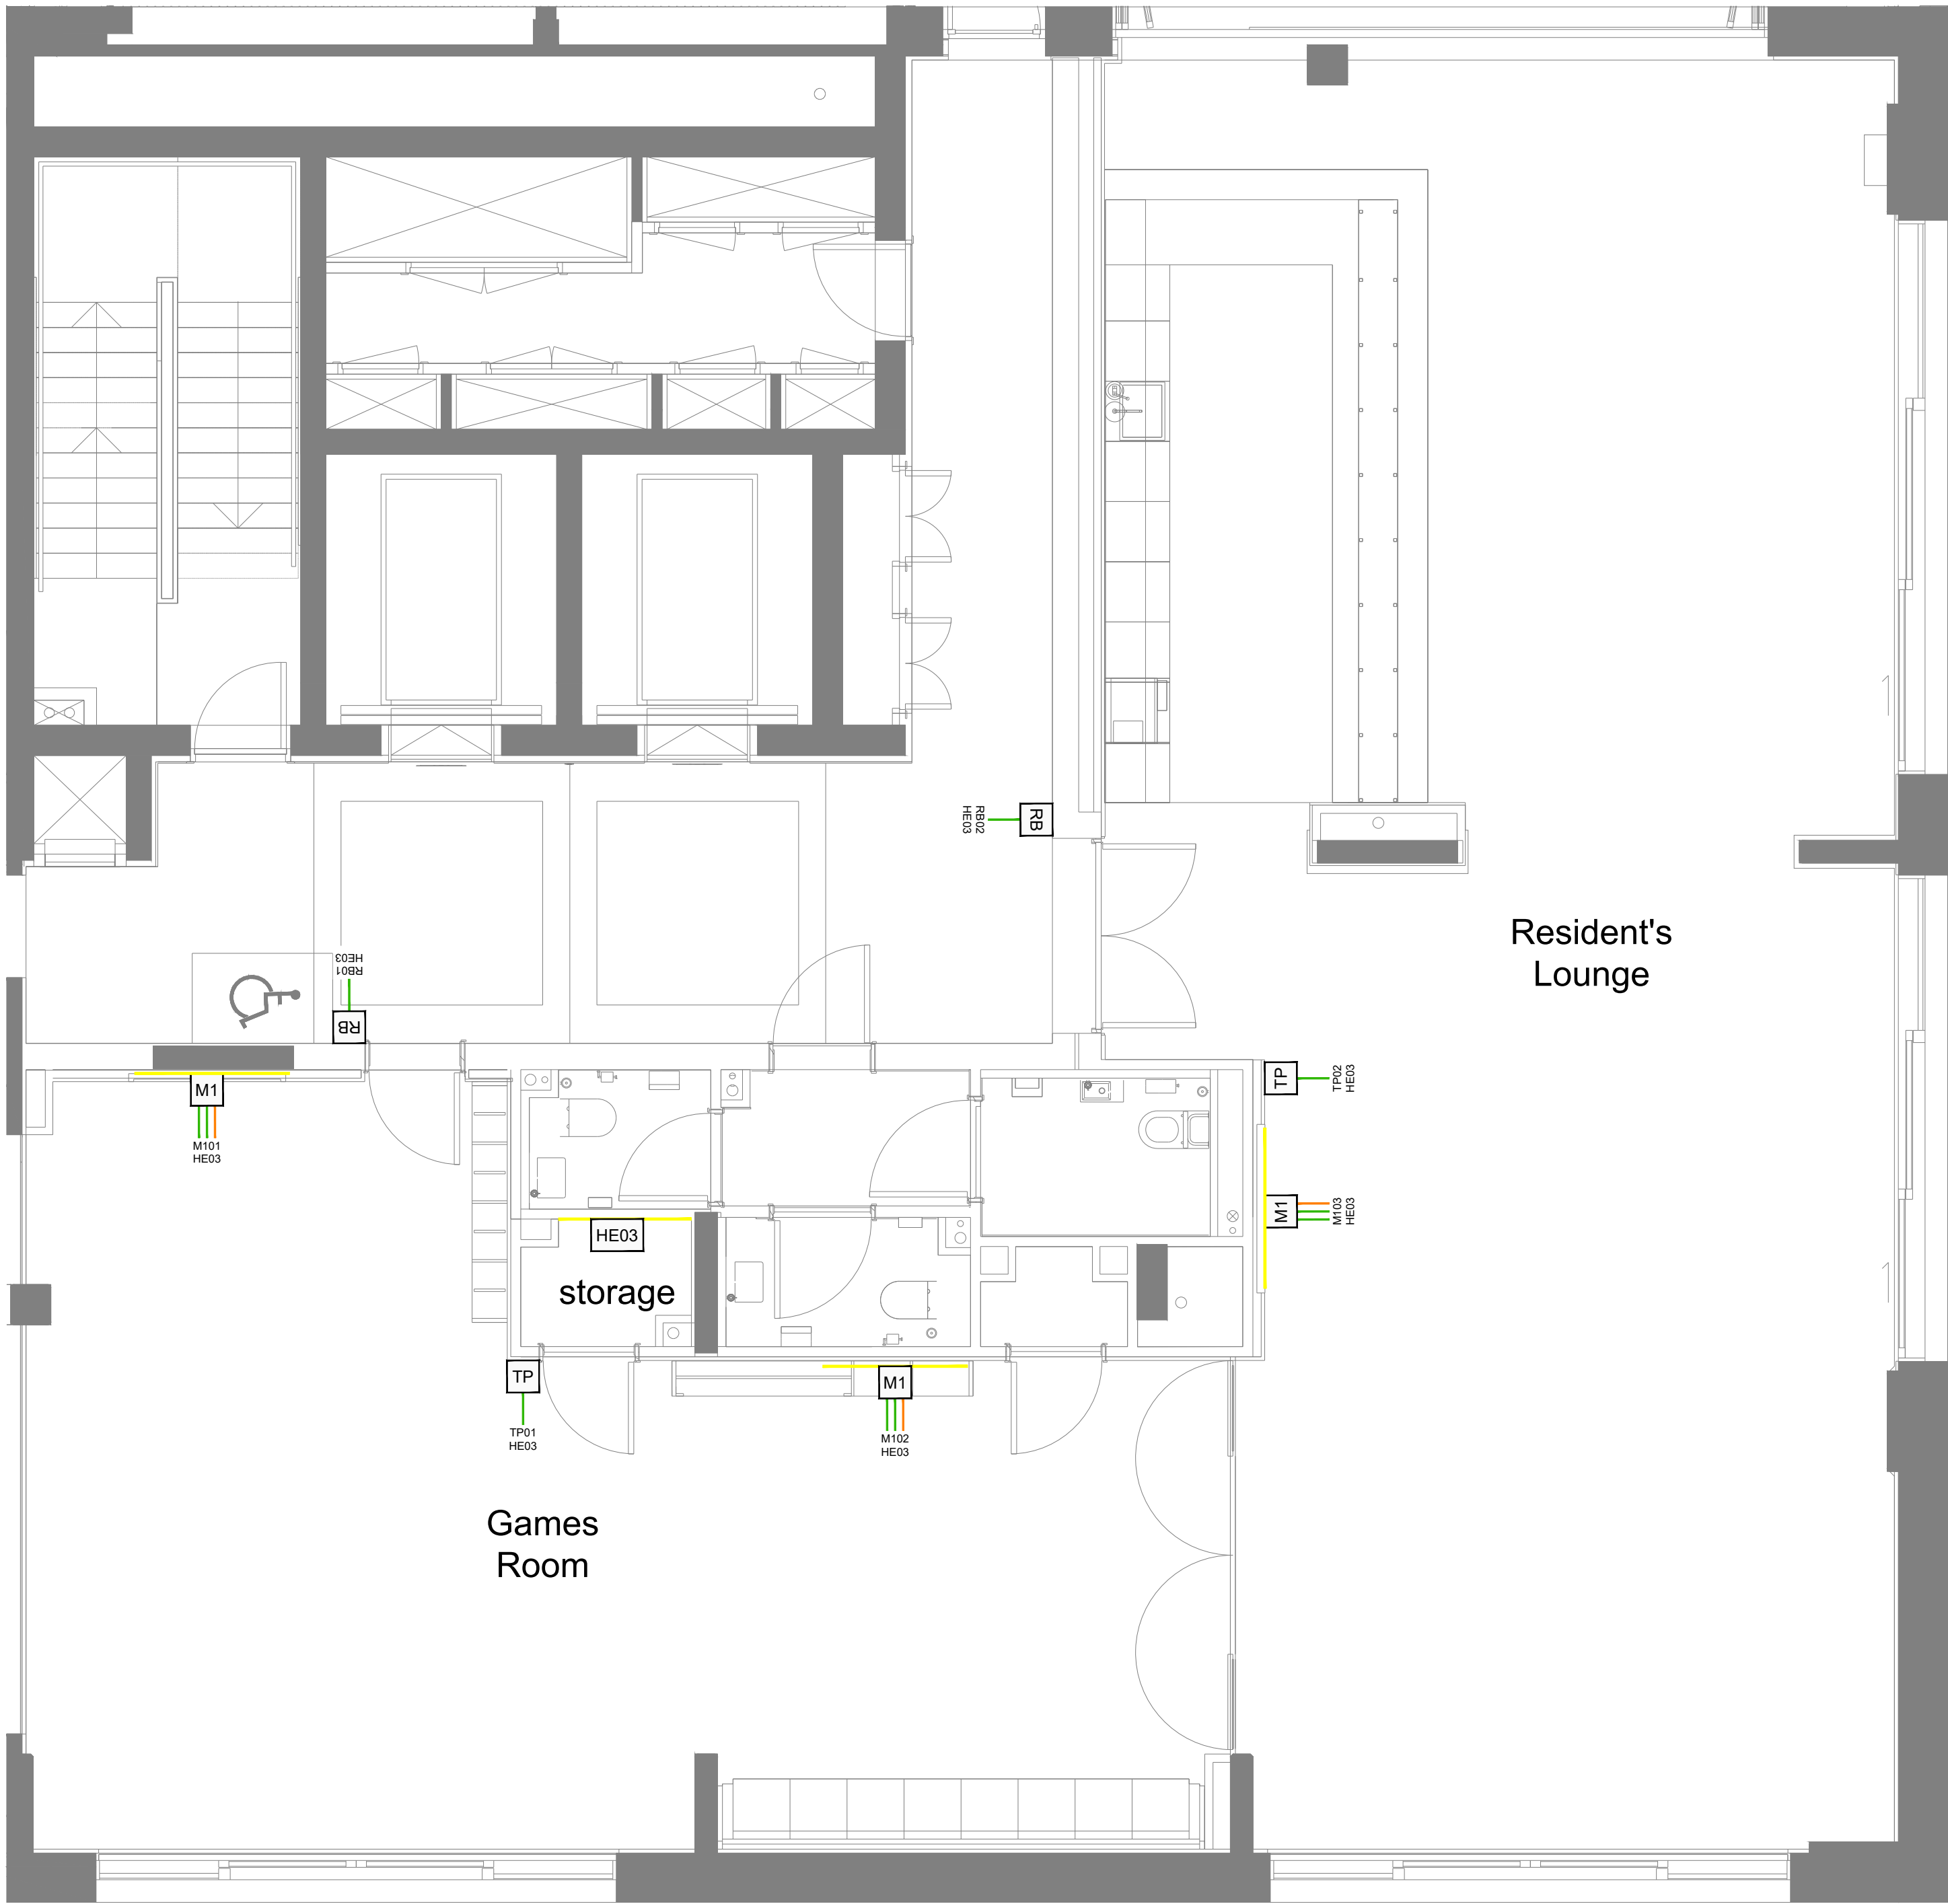

NOTES

Reference Drawings

17010_AAM_BB_10_DR_A_06110.C15.20 (GA)

LEGEND

Item Example

M1 "M1" Wall Mounted Media Plate 01
M102 "Cables" 2x CAT6a and 1x WF100
HE01 "M1" Item ID "02" Unique Number
HE01 "HE01" Head End

Head End Equipment

HExx Wall Rack
By Others
- LV (230V) Power
- Fire Alarm Interface(s)
- HVAC Cooling
- Landlords Network Connection(s)

Wall Mounted Equipment

M1 Media Plate 01
By Others
- LV(230V) Power

RB Room Booking Panel

TP Touch Panel

FP Fire Place

Speaker Types

S1 Speaker Type 1 - Ceiling

S2 Speaker Type 2 - Wall Mount

S3 Speaker Type 3 - External

S4 Speaker Type 4 - External

S5 Speaker Type 5 - External Wall Mount

S6 Speaker Type 6 - Soundbar

S7 Speaker Type 7 - In-Wall

S8 Speaker Type 8 - In-Wall

S9 Speaker Type 9 - Ceiling

Floorboxes

FB Floorbox

Cable Types

Speaker Cable
TBC
CAT6a Cable F/FTP
Nexans (N100.692G-OC)
WF100 Digital Coaxial Cable
Weibro (392100HCAI)
HDMI Cable
TBC
Power cable (230V) from UPS
TBC

For Construction

© Copyright. All rights to this drawing and its design are the property of SmartComm Ltd. Any use or duplication of this drawing is strictly prohibited without prior written permission of SmartComm Ltd.

Drawn By	SD	19/06/23	
Checked By	CL	19/06/23	
Issued By	SD	19/06/23	

SCALE NTS

PAGE SIZE A1

smartcomm
integrating technology with vision

Smartcomm Ltd
Holford Road
Cresswell Business Park
High Wycombe
Buckinghamshire
HP12 3SN
Tel: +44 (0)1494 471 912
E-mail: info@smartcomm.co.uk
Web: www.smartcomm.co.uk

C02	For Construction	19/06/23	SD
C01	For Construction	13/10/22	SD
A01	For Information	12/05/22	SD
Rev	Description	Date	Name

Royal Mail Parkside
Block B Level 10
AV Layout - Low Level

Project	Section	Type	Number	Revision	Version
NEPS	BB-10	GA	01	C02	V03